
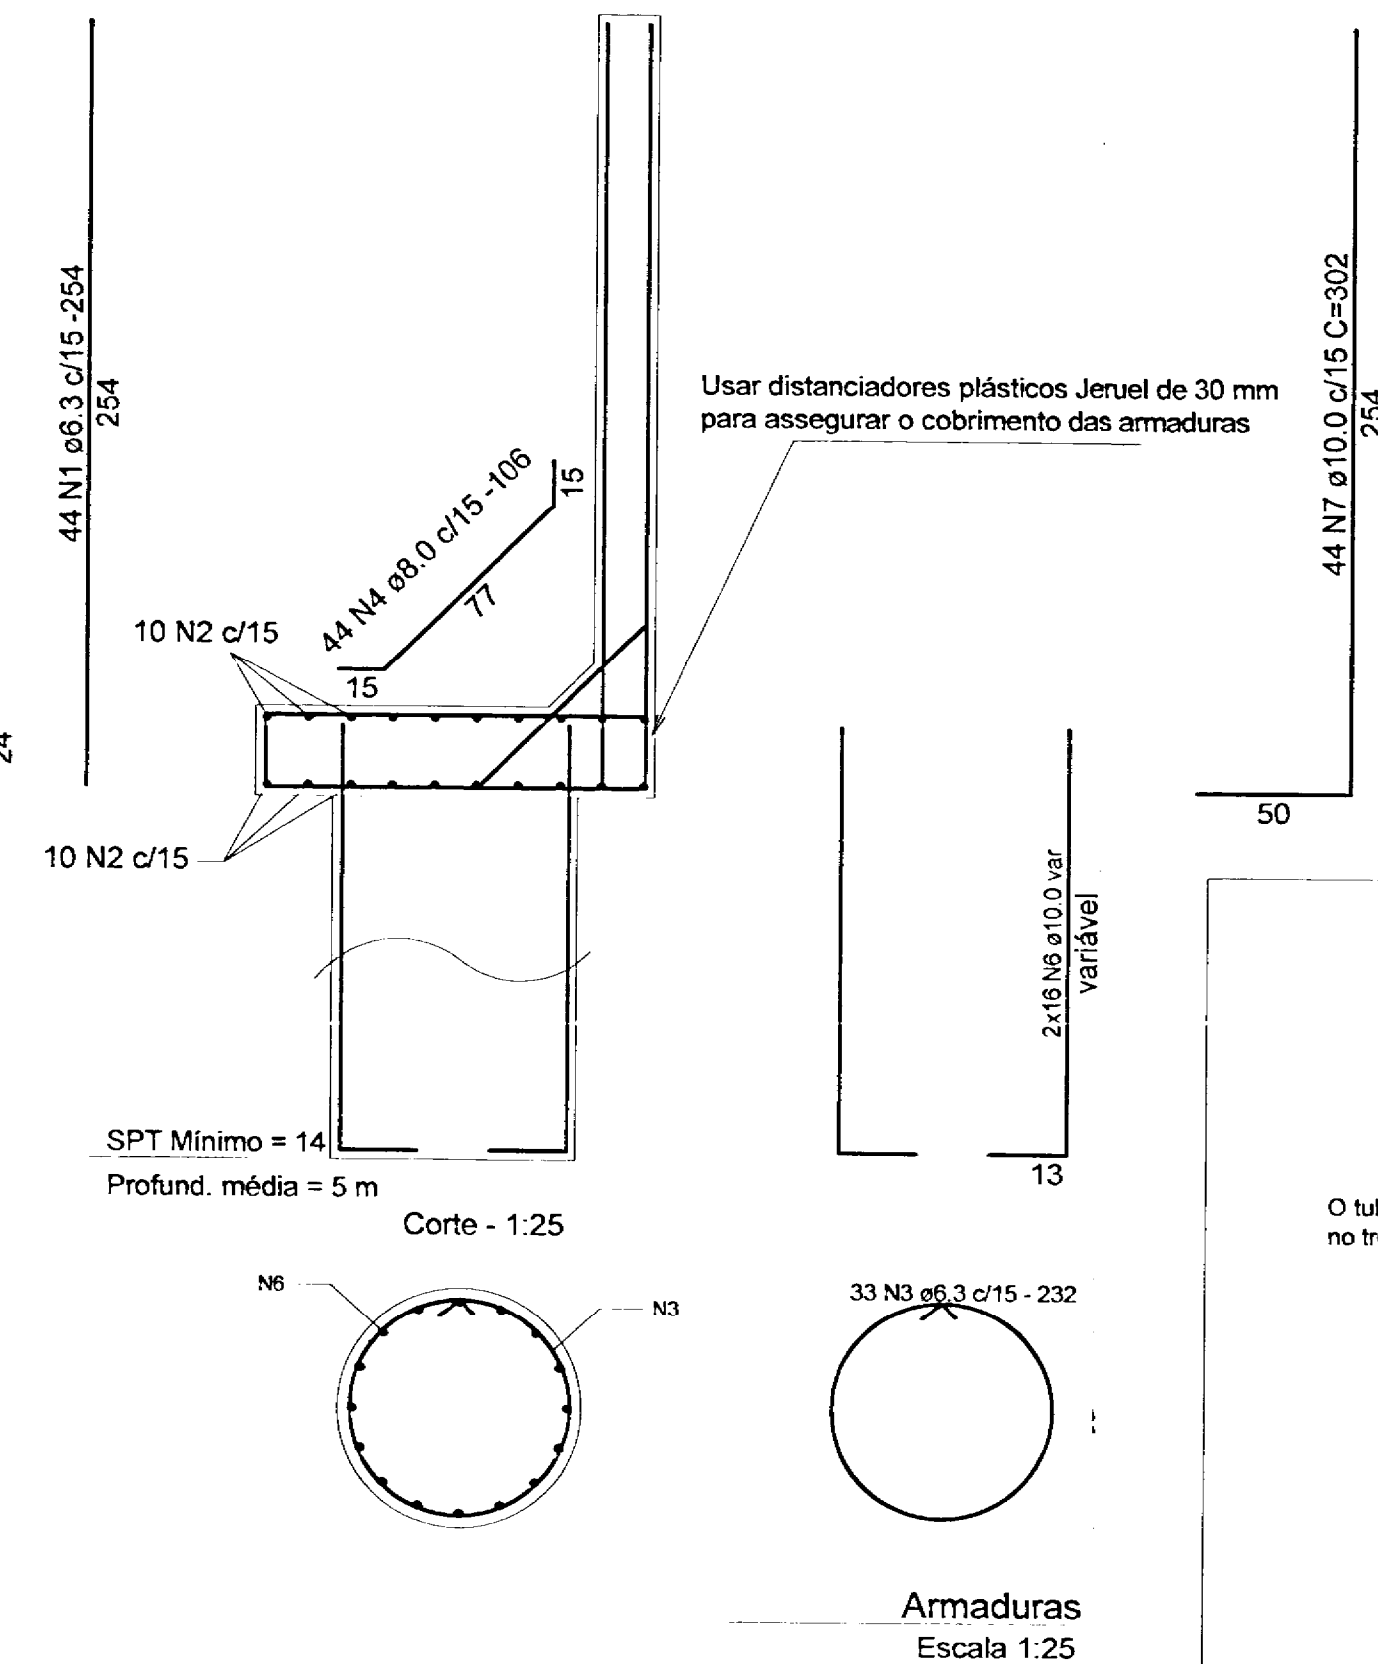
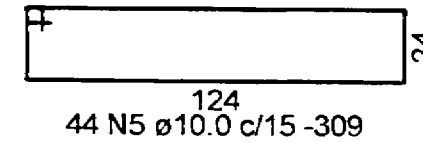


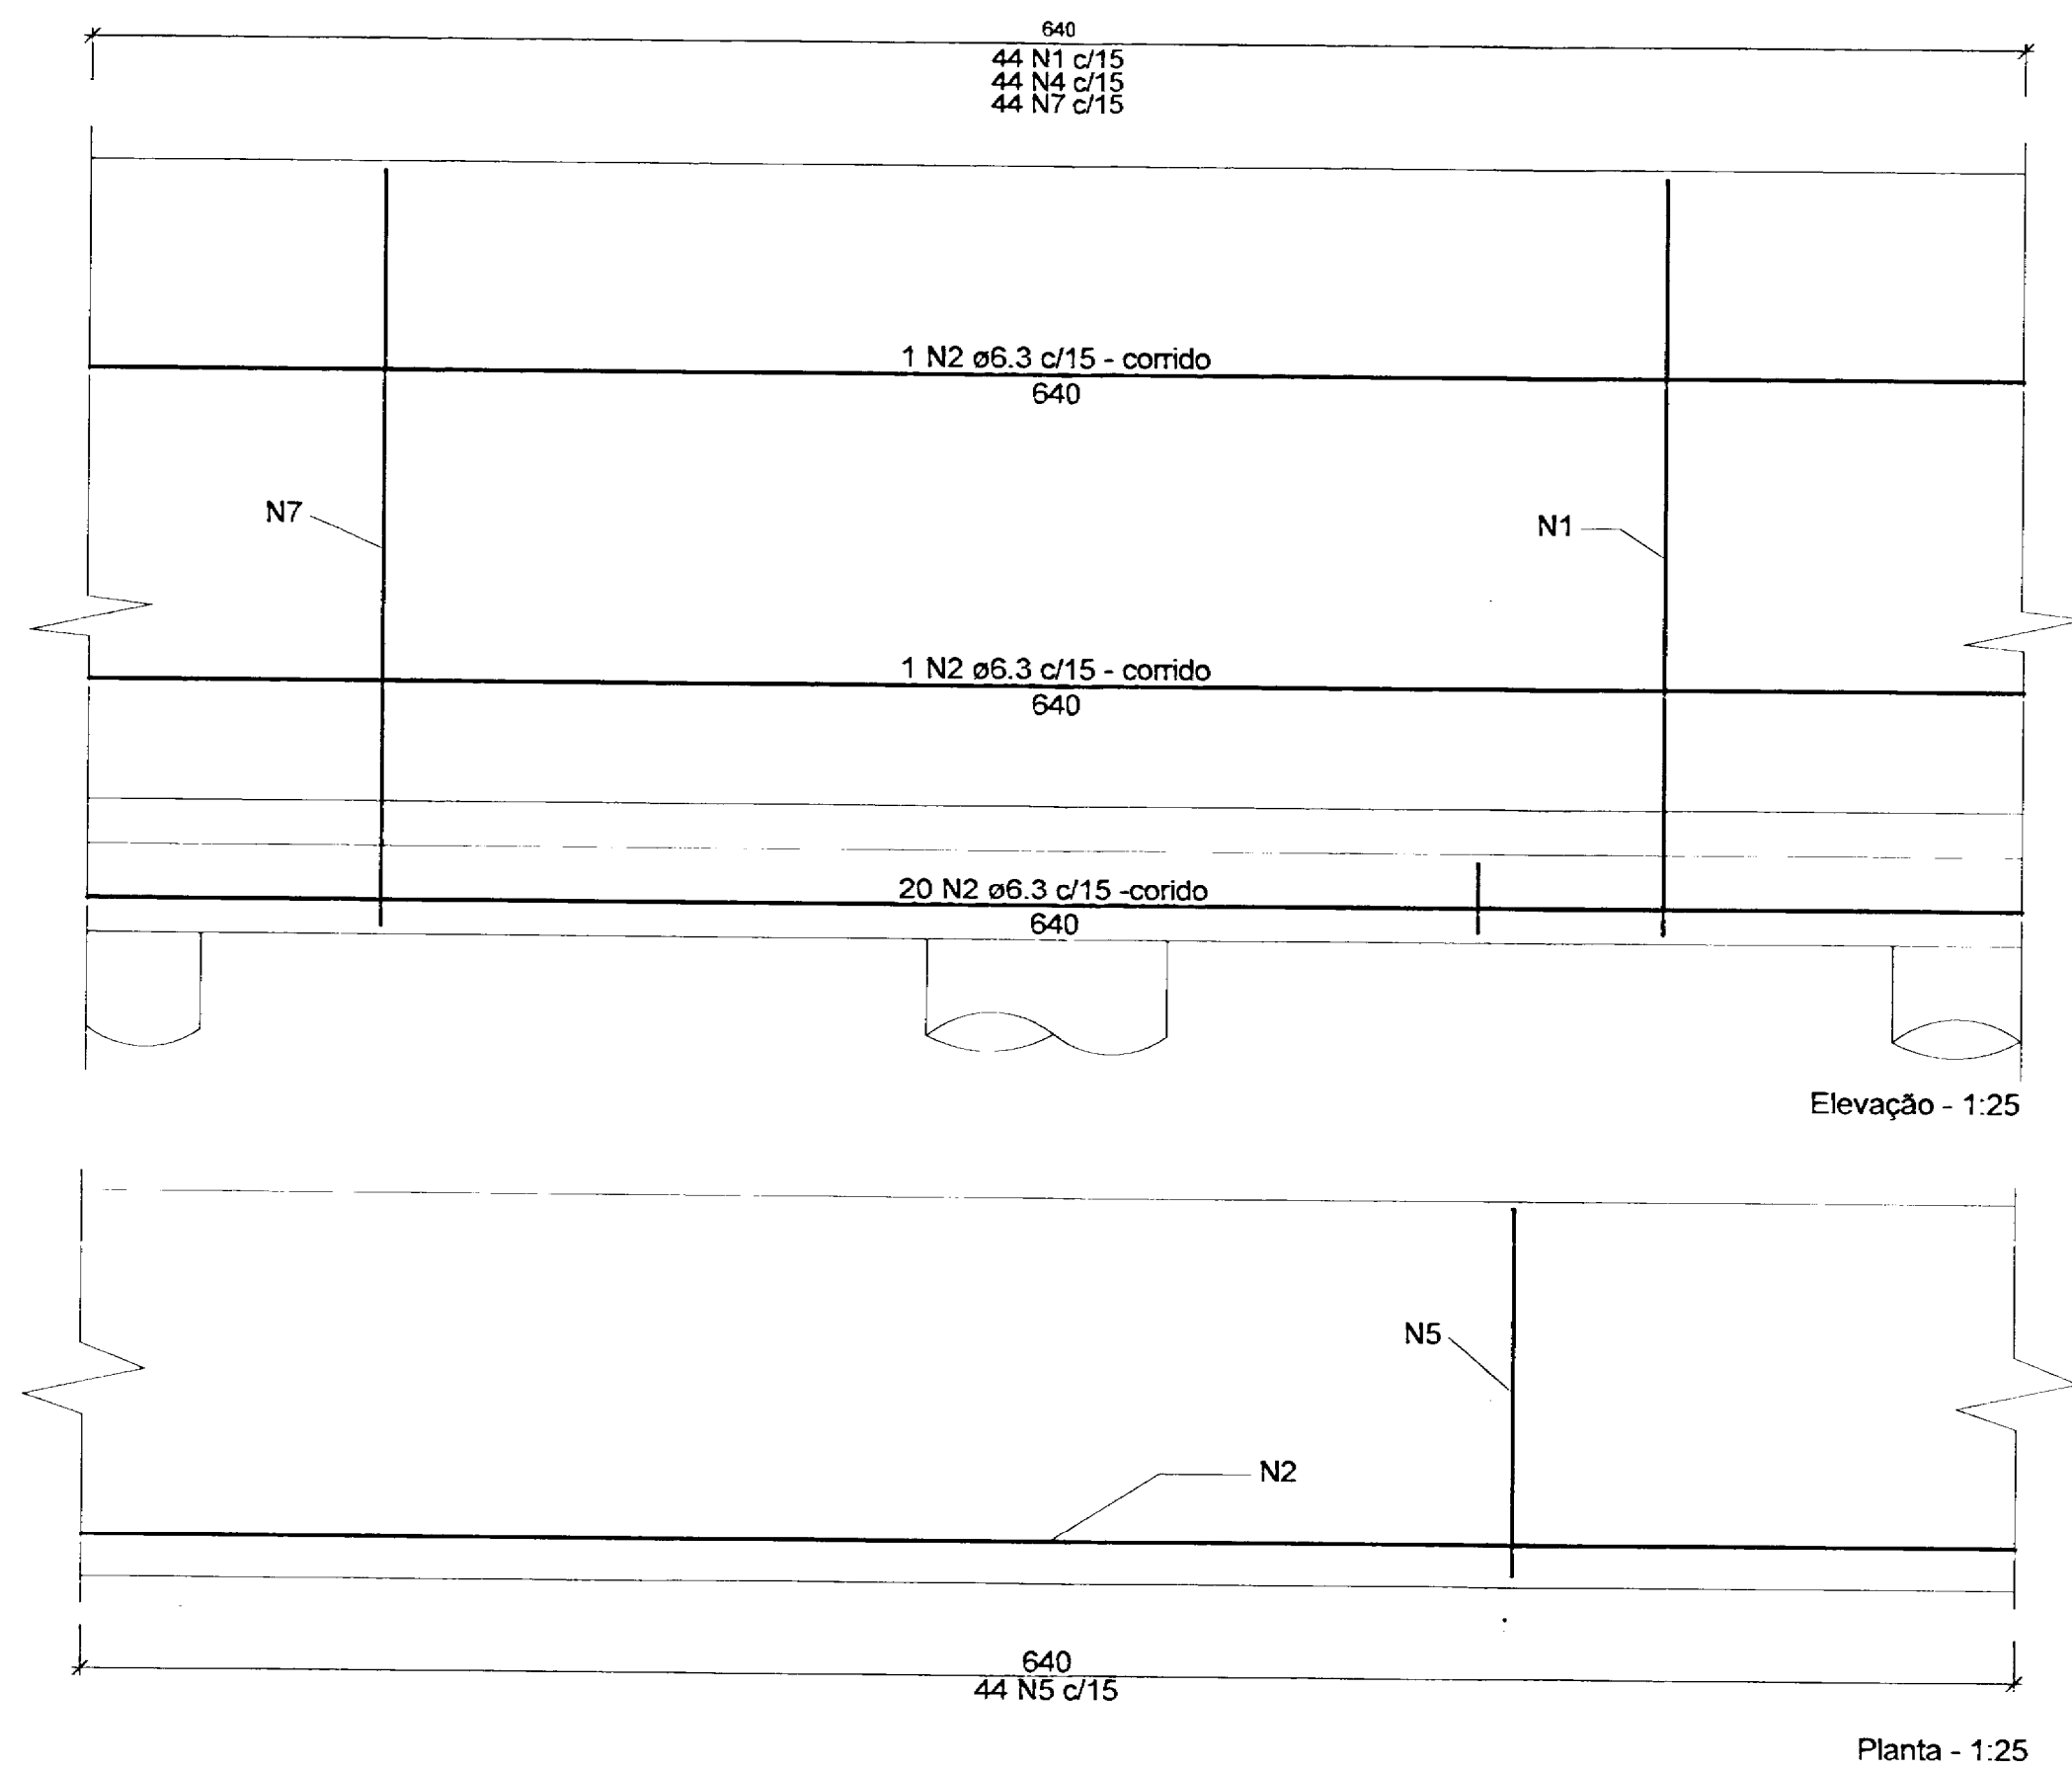




Relação do aço

AÇO	N	DIAM	Q	UNIT (cm)	C.TOTAL (cm)
CA50	1	6.3	44	254	11176
	2	6.3	22	640	14080
	3	6.3	33	232	7656
	4	8.0	44	106	4664
	5	10.0	44	309	13596
	6	10.0	32	var	16000
	7	10.0	44	302	13288

Resumo do aço

AÇO	DIAM	C.TOTAL (m)	PESO + 10 % (kg)
CA50	6.3	329,1	88,6
	8.0	46,7	20,2
	10.0	428,8	290,7
PESO TOTAL			
CA50		399,5	

Quantitativos calculados para um módulo de 6.4 m

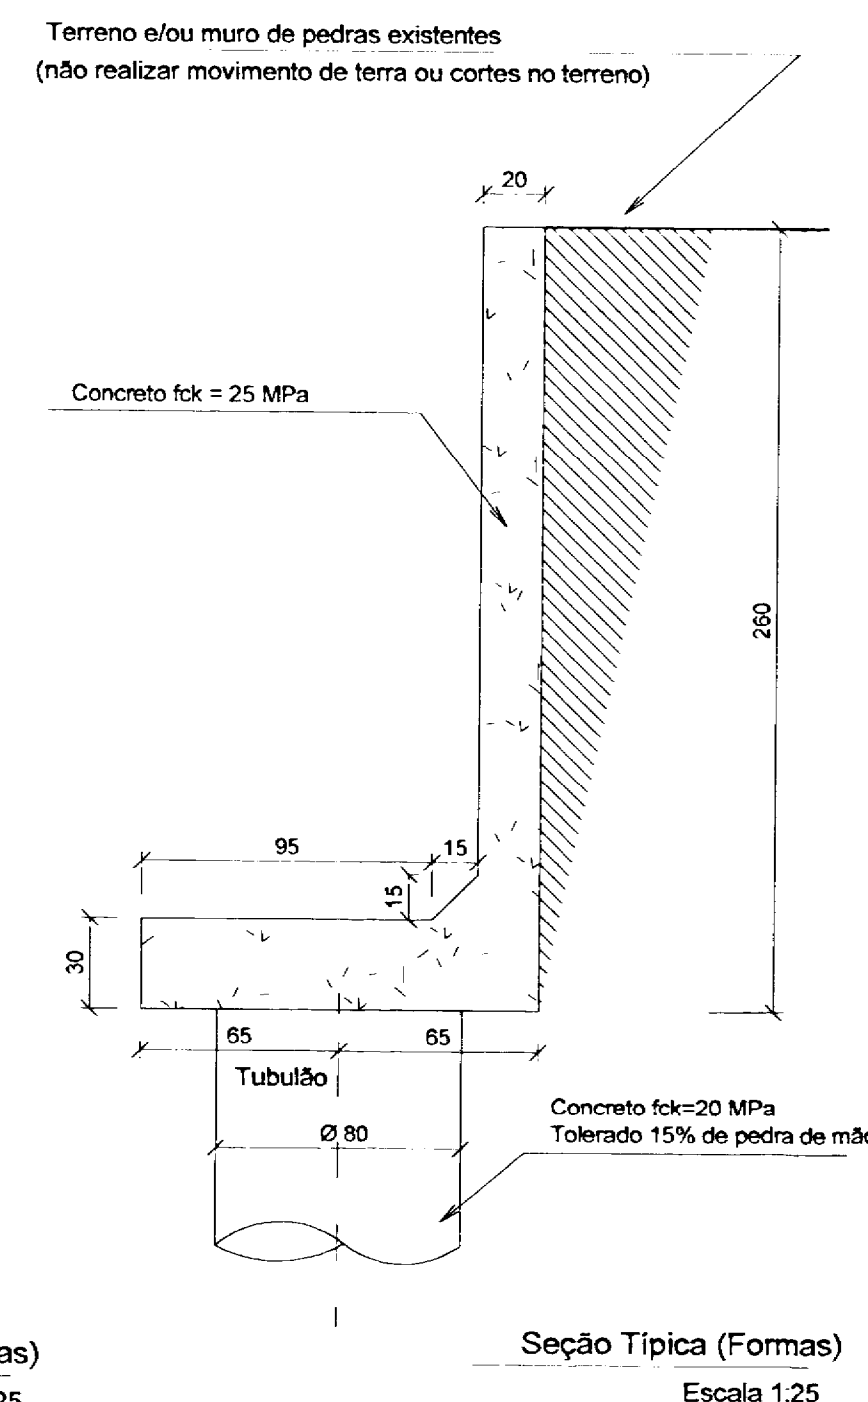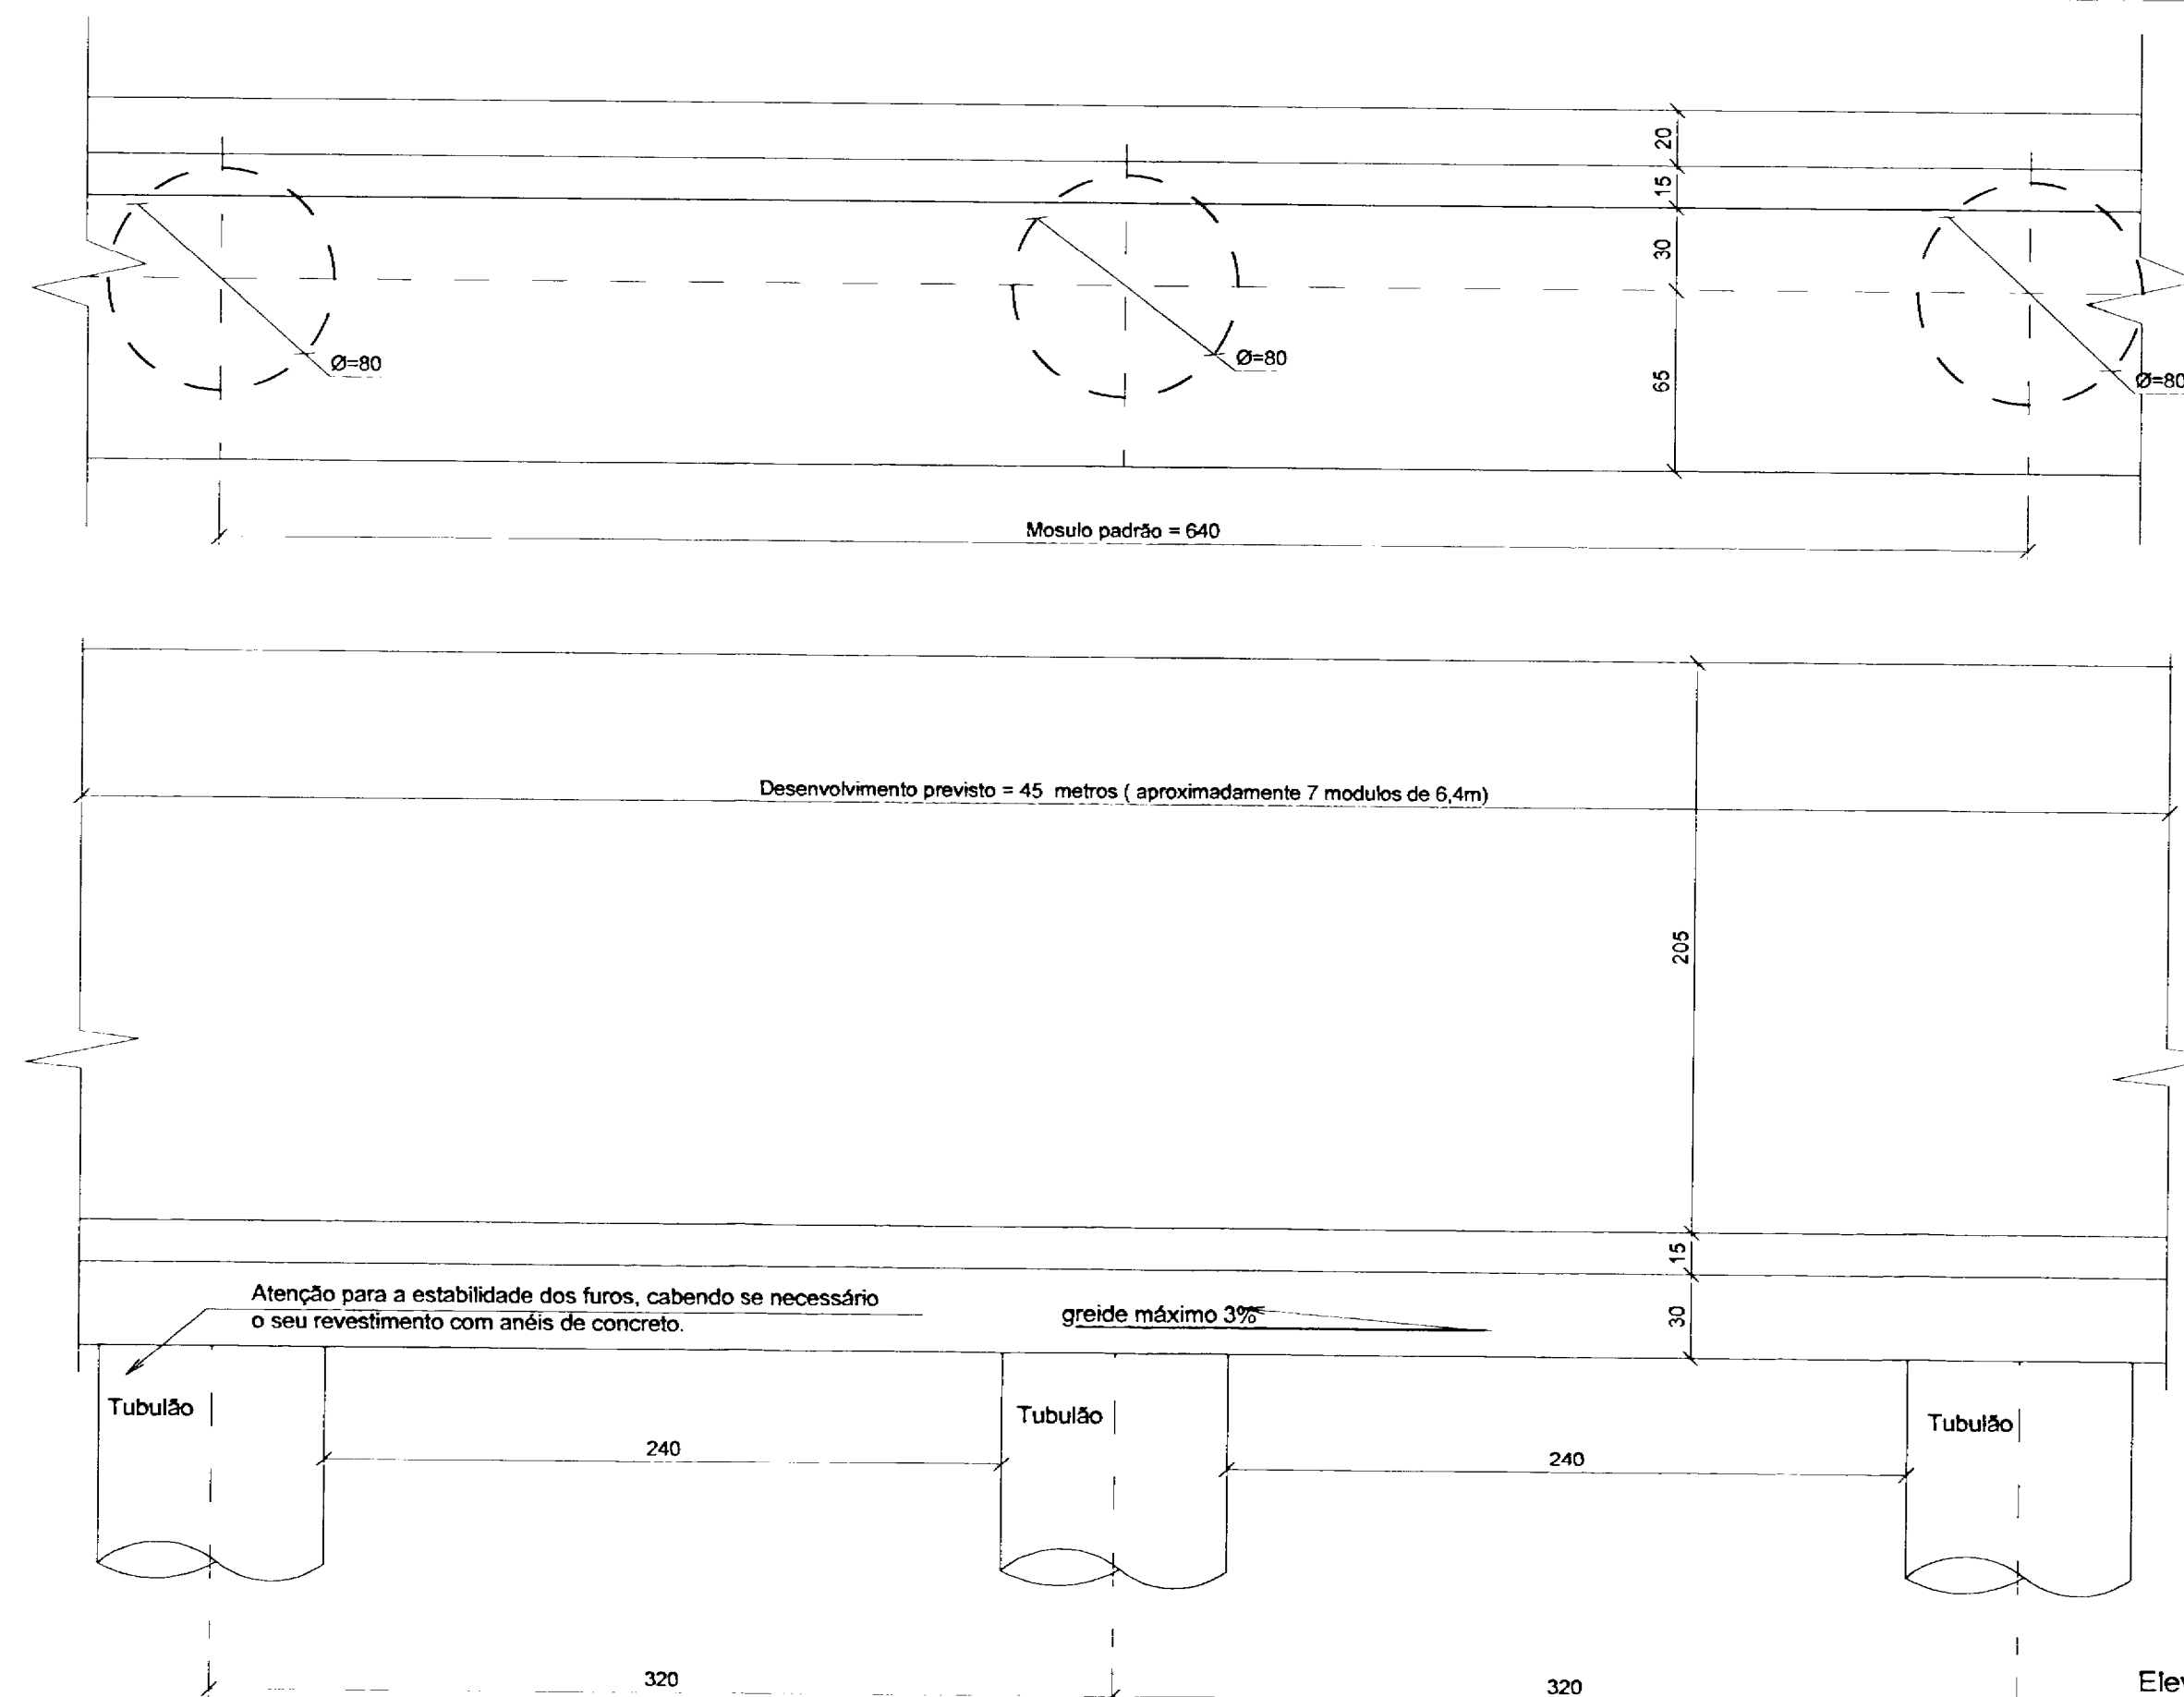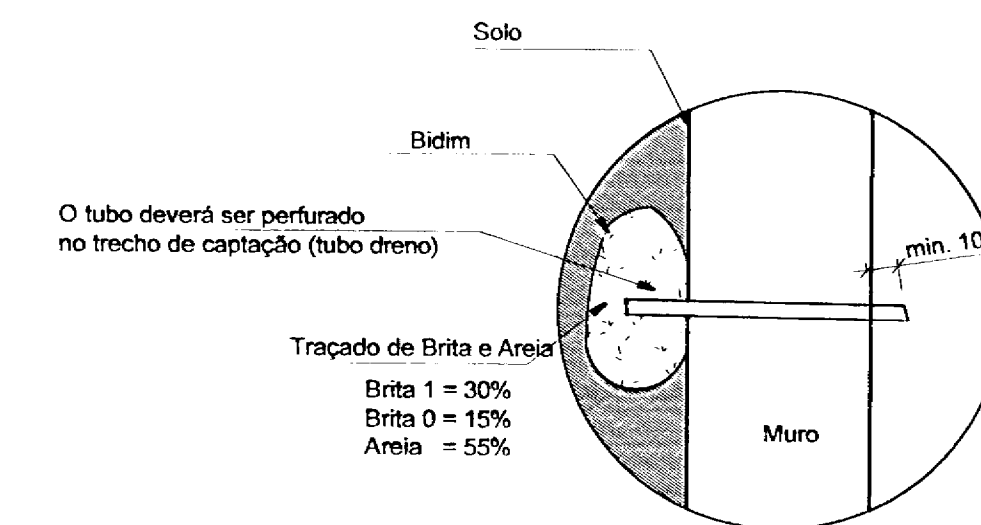

Notas do Autor

- 1- A estabilidade do muro em questão dependerá da manutenção permanente dos sistemas de drenagem a montante, sendo necessária a revisão periódica da condução das águas provenientes das calhas da residência e sistemas de esgoto.
- 2 - Os trechos onde atualmente existem muros de pedra sem função estrutural, poderão ser utilizados com fins de formas para o novo muro.
- 3 - O projeto estrutural esta baseado nas informações contidas no Boletim de Sondagem SP/AE/2119 executado pela empresa Solobase. A presença de grandes falhas ou fendas de origem geológica não detectadas pelo ensaio de SPT, fazem com que o efeito da contenção seja assegurado de forma local, na região da piscina e decks.
- 4 - Considerou-se, em função da distancia, que as fundações da residência não exerçam pressões sobre o muro em questão e que a ação de seu bulbo de pressões encontre-se abaixo do nível to topo do muro.
- 5 - A altura do muro pode sofrer variações a menor em função da passagem pelos decks de madeira existentes. Qualquer modificação que se faça necessária para a perfeita adequação do projeto ao local, so poderá ser feito com autorização por escrito do Autor do Projeto.
- 6 - O local de aplicação do presente projeto encontra-se caracterizado na prancha 2 que faz parte integrante deste projeto.
- 7 - As fundações dos decks deverão ser revisadas no local onde ocorreu intensa infiltração de água, bem como região de recalques previamente existentes.

N		Data	Histórico	Revisado por
REVISÕES				
PROJETO ESTRUTURAL				Prancha
CLIENTE : Ametista Participações ENDEREÇO : Rua Virginia Ribeiro, 1865 Nova Friburgo - RJ				01
ESCALA	DESENHO	DATA		
Indicada	Marcello	Junho/07		
PROJEMART ENGENHARIA LTDA MARCELLO MARTINS Engenheiro Civil - Crea 86101793-6 Rua Ernesto Brasilio, 64 sala 211 - Centro Nova Friburgo - RJ Tel Fax (22) 2522 9529 - 2521 0778				Autorização Desenho válido somente com assinatura em original