


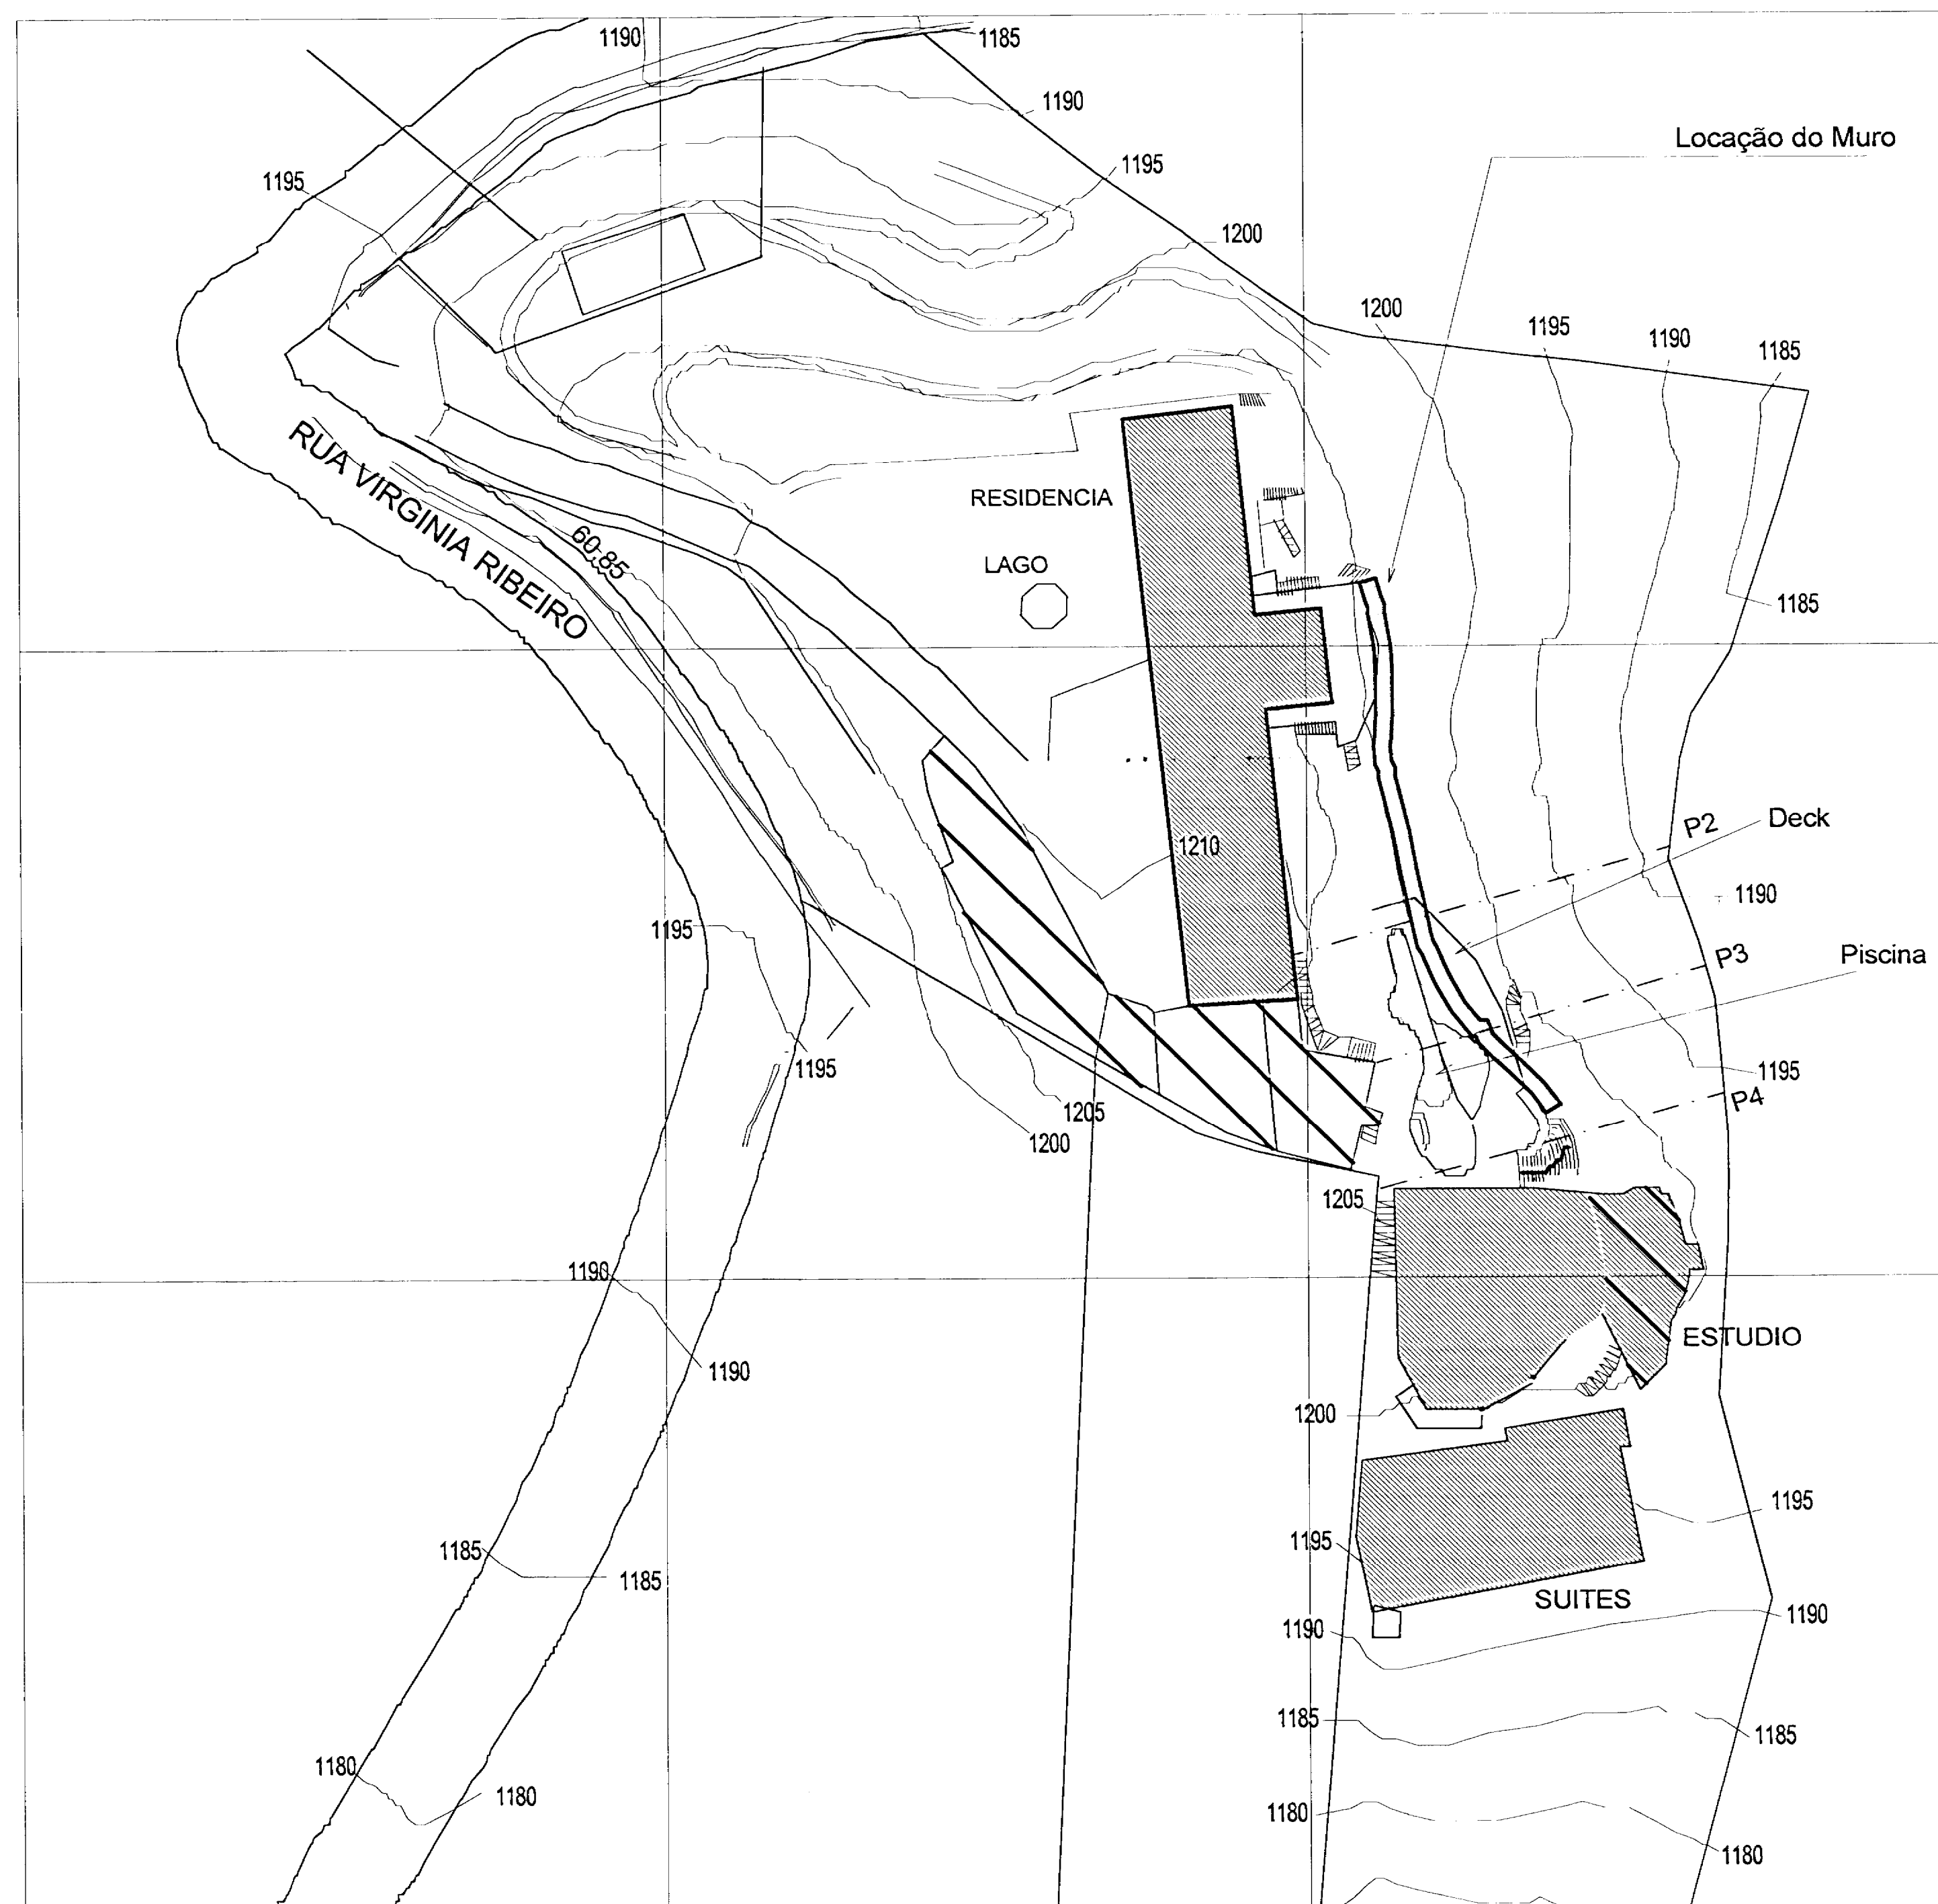

Locação do Muro

RESIDENCIA

LAGO

P2 Deck

1190


P3 Piscina

P4


ESTUDIO

SUITES


Locação
Escala 1:400

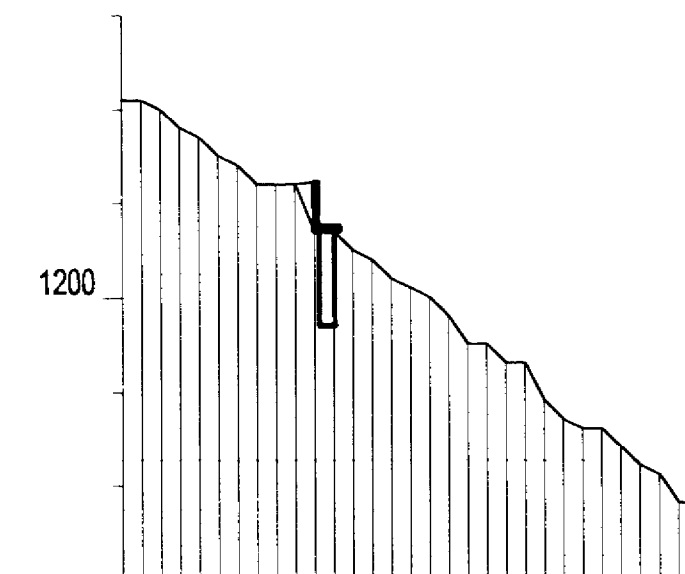

Seção P2
Escala 1:400

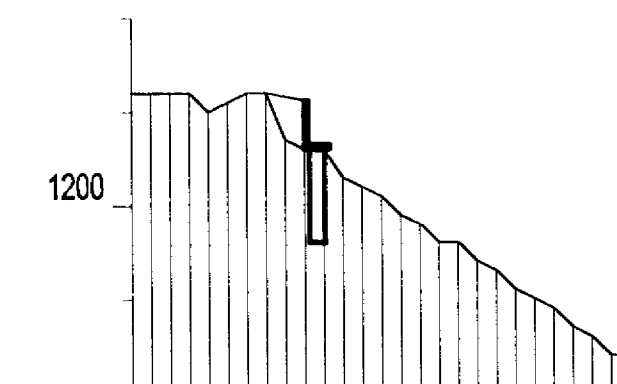

Seção P3
Escala 1:400

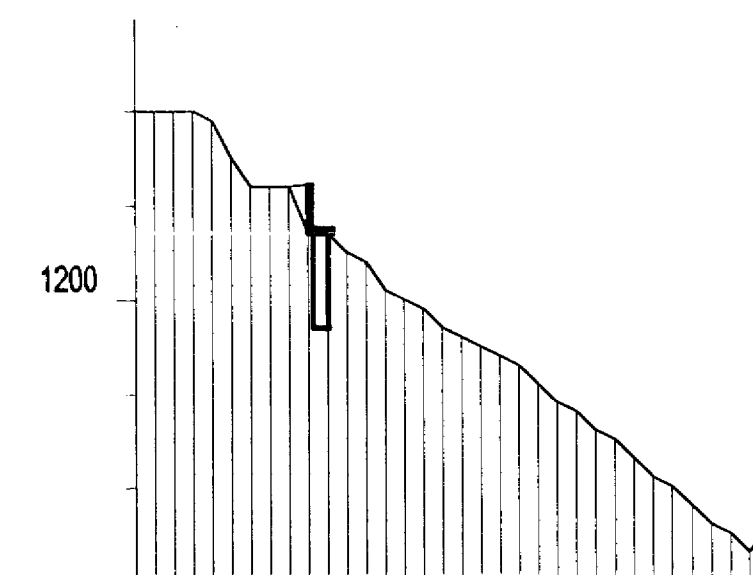

Seção P4
Escala 1:400

Vide Notas do Autor na Prancha 01

N	Data	Histórico	Revisado por
REVISÕES			
PROJETO ESTRUTURAL			
CLIENTE : Ametista Participações ENDEREÇO : Rua Virginia Ribeiro, 1865 Nova Friburgo - RJ			Prancha
ESCALA Indicada	DESENHO Marcello	DATA Junho/07	02
PROJEMART ENGENHARIA LTDA MARCELLO MARTINS Engenheiro Civil - Crea 86101793-6 Rua Ernesto Brasileiro, 64 sala 211 - Centro Nova Friburgo - RJ Tel Fax (22) 2522 9529 - 2521 0778			
Autorização			Desenho válido somente com assinatura em original