




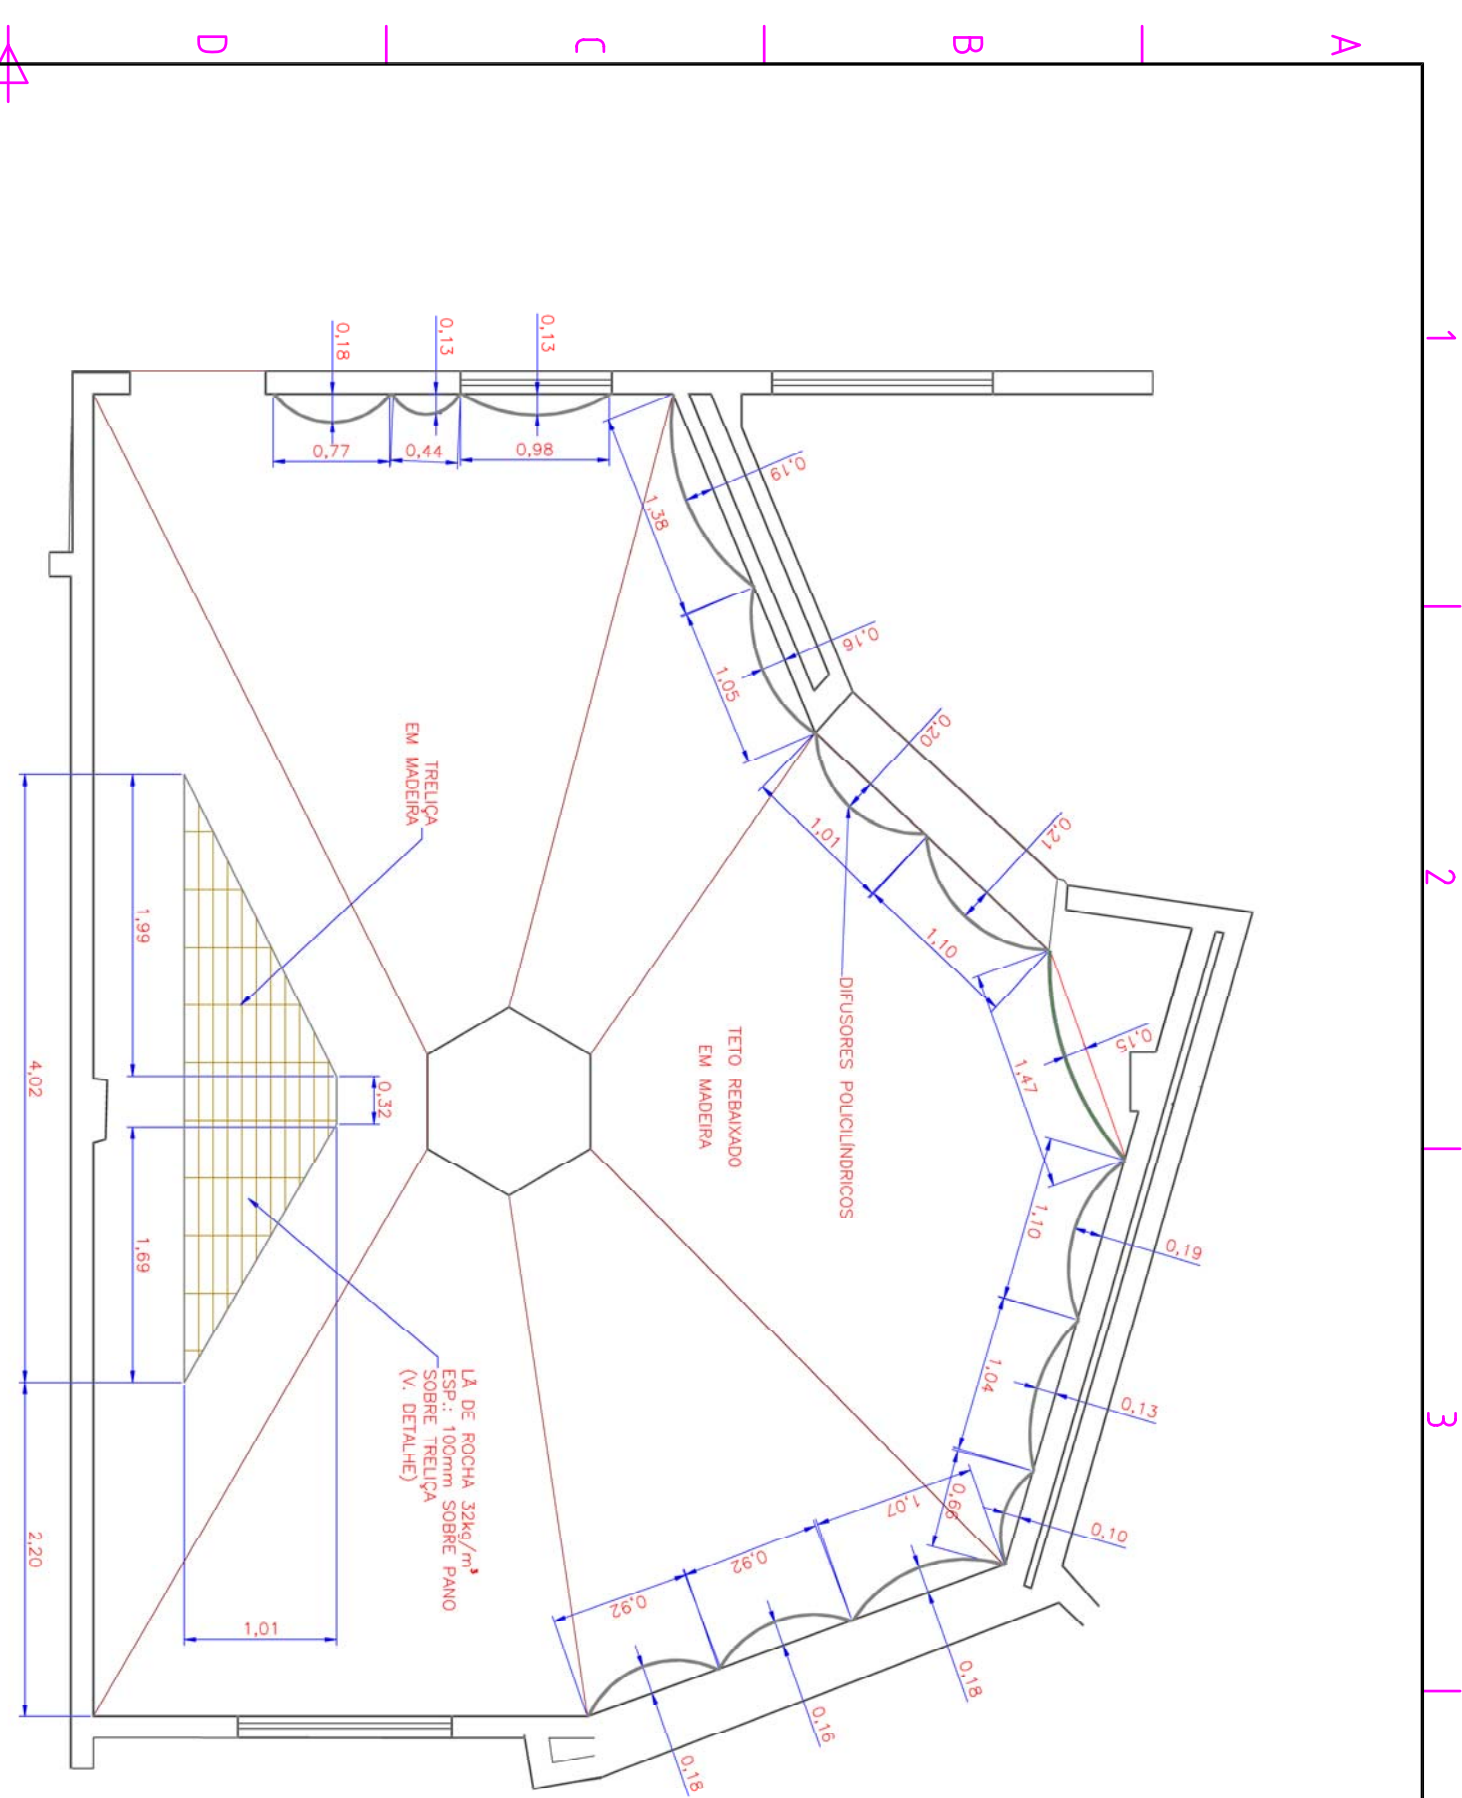

SUPERIOR

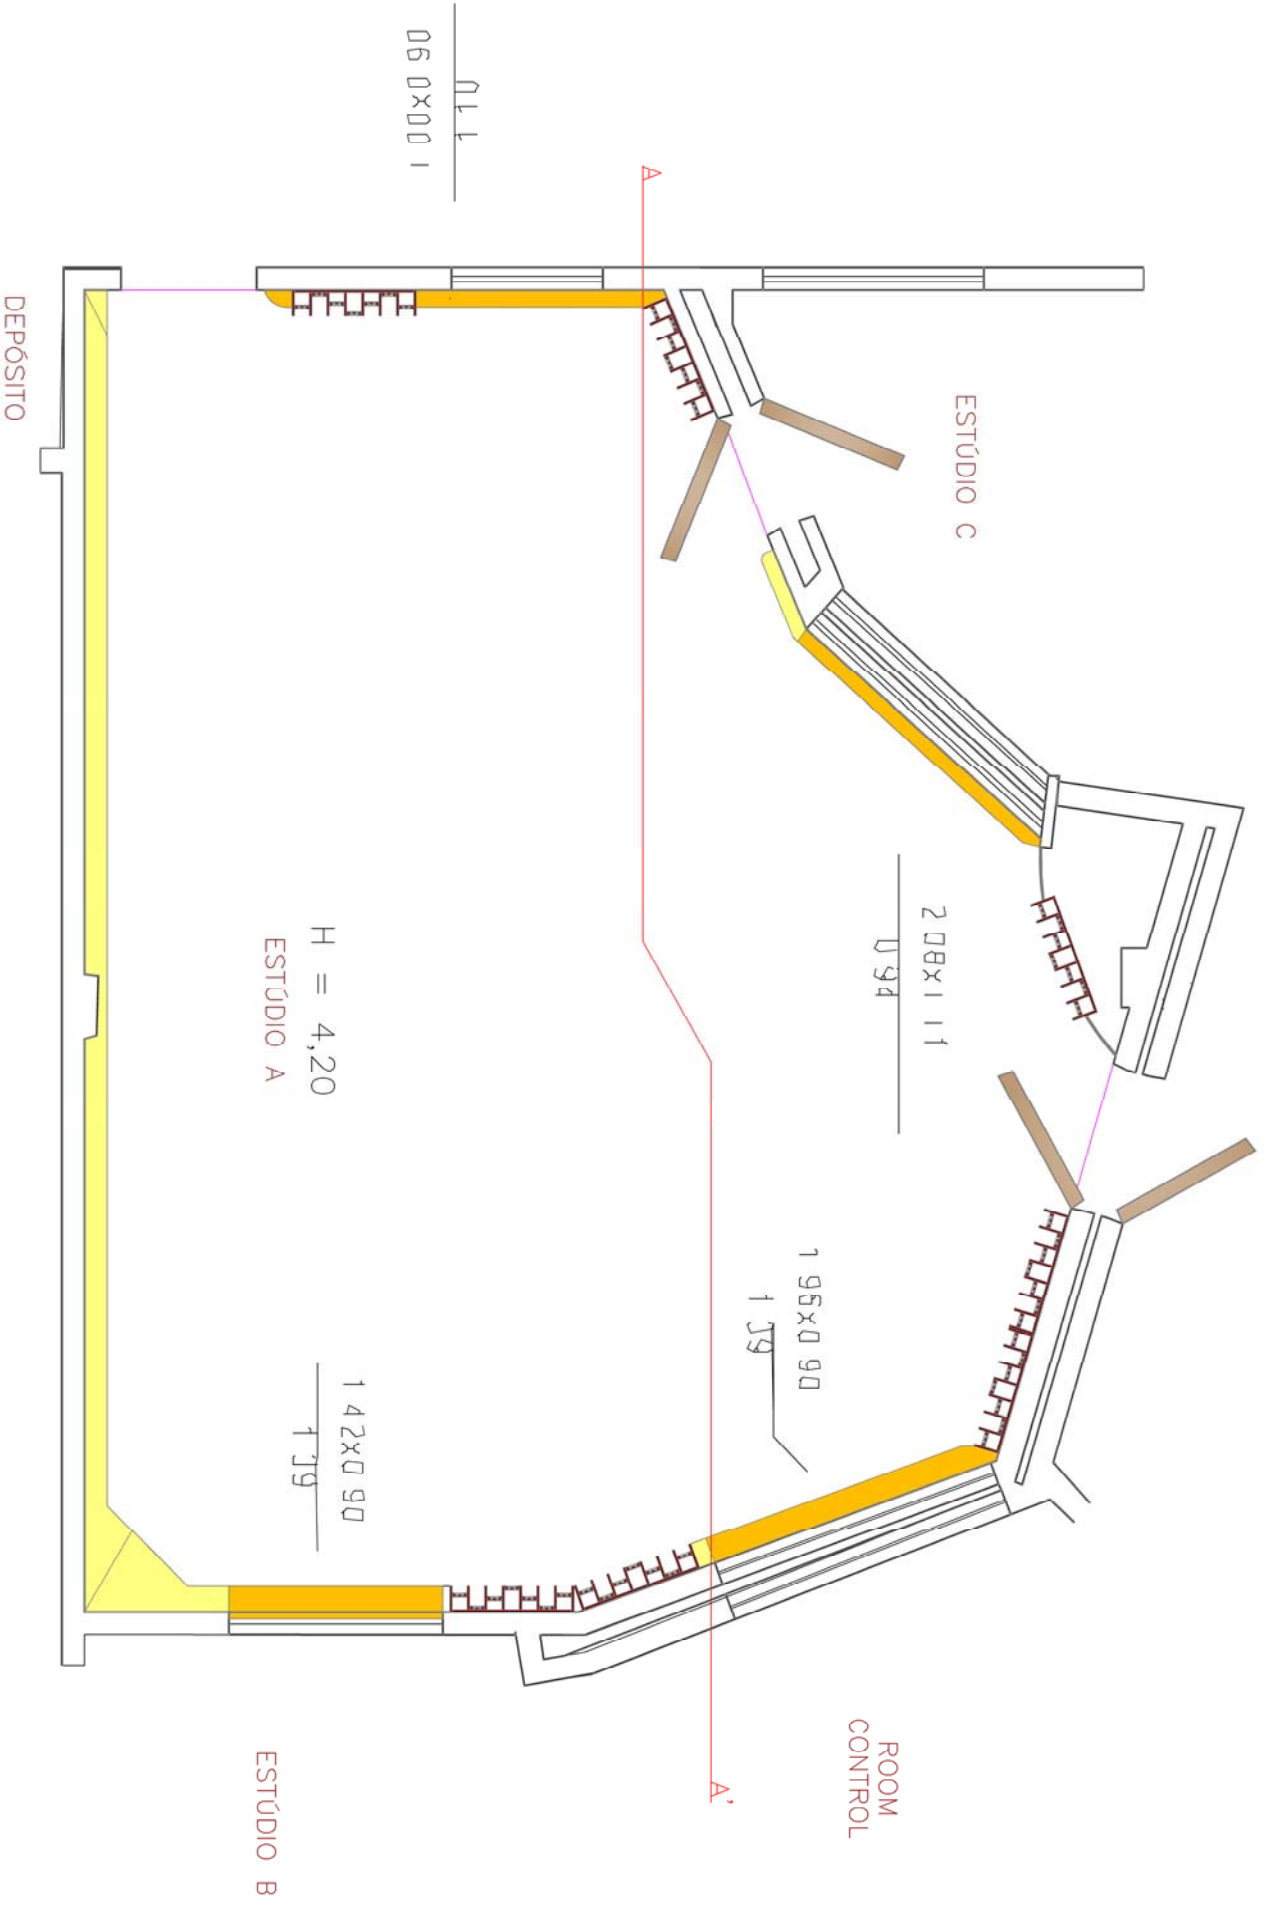

INTERIOR

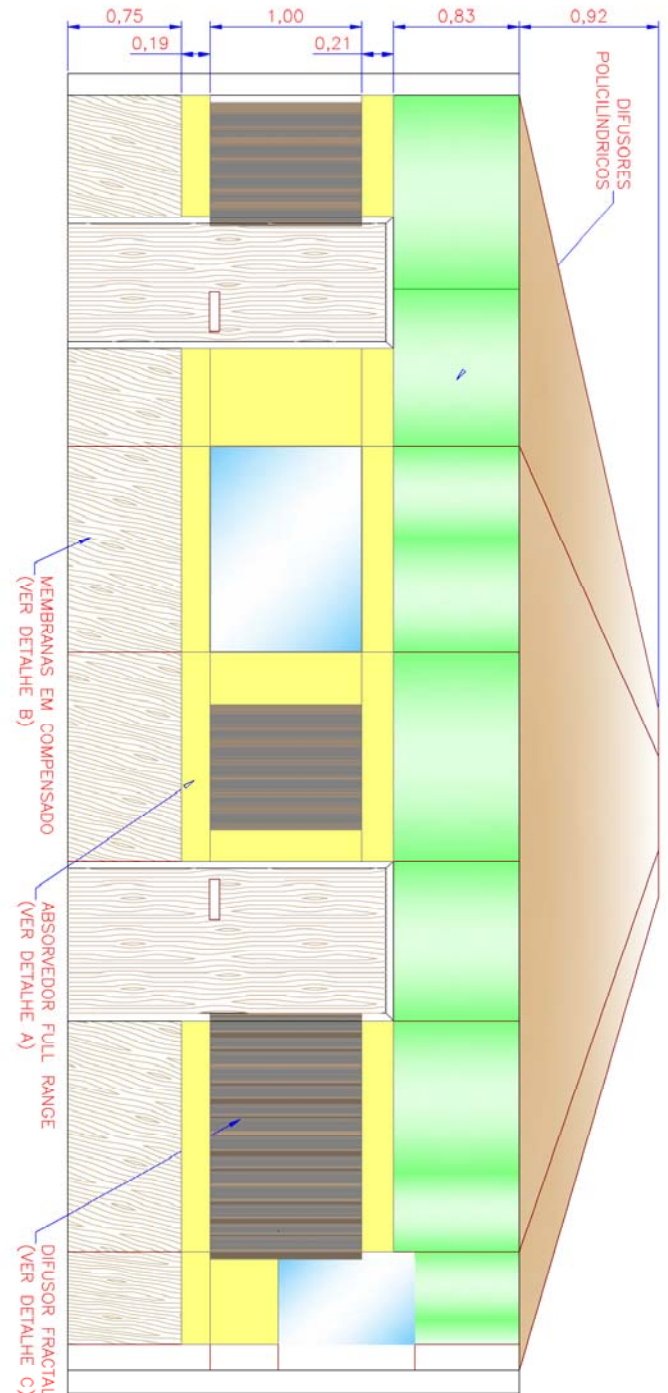

CORTE AA'

solon do valle

ESTÚDIO DA MONTANHA

ESTÚDIO A		ESTÚDIO B	
DATA:	05/02/07	TRATAMENTO ACÚSTICO	1.0
ESCALA:	1:20	PAREDES, TETO E VISORES	PROJETO:
		LOCALIZAÇÃO	