


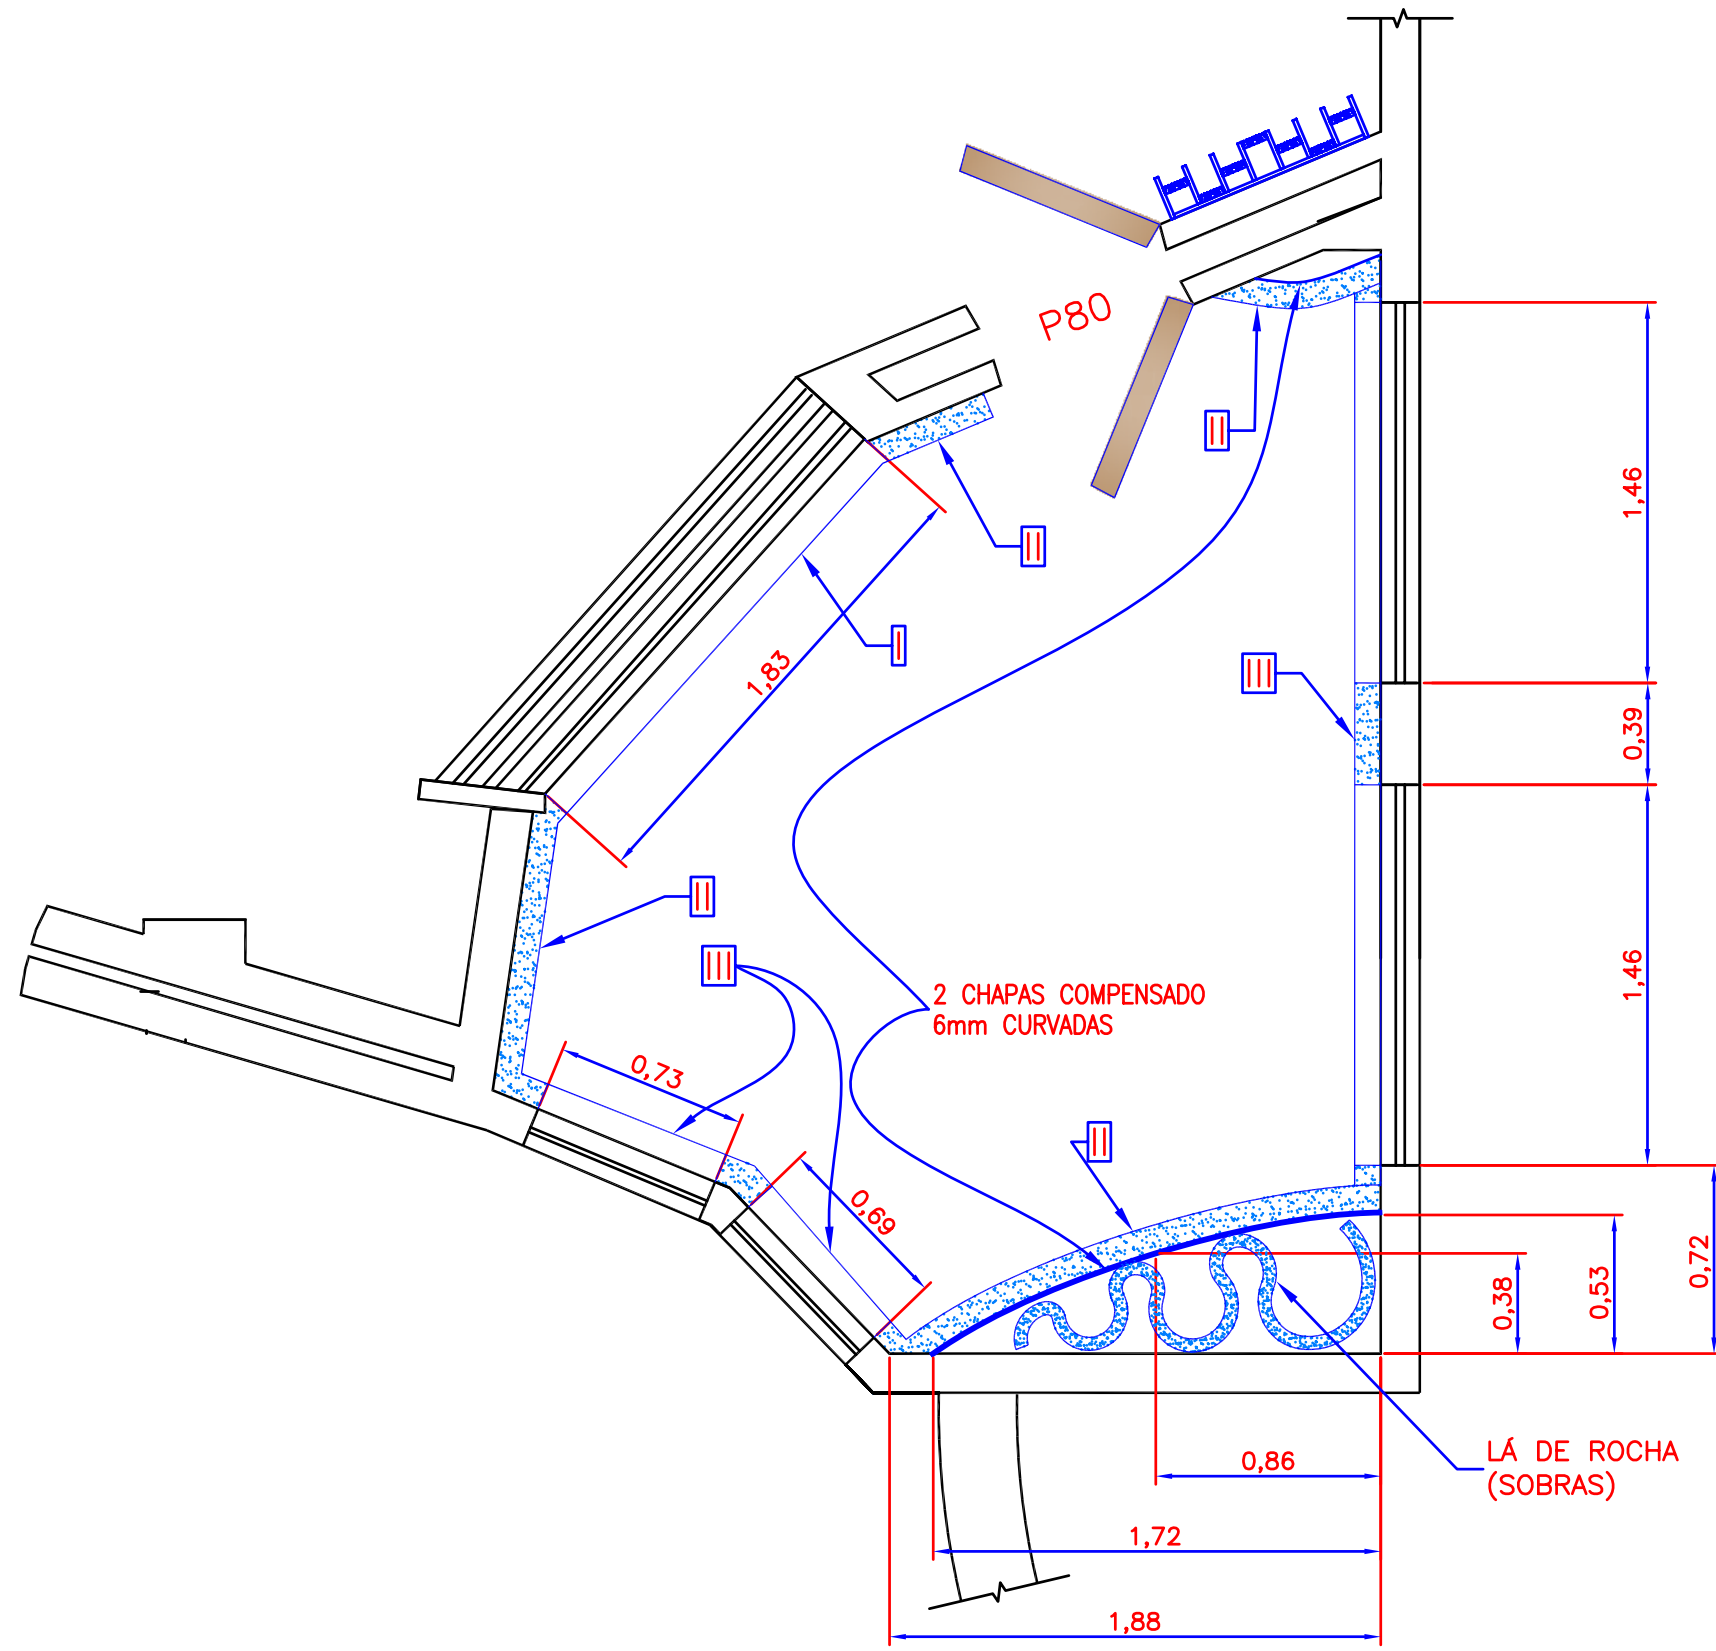

ESTILOS DE ACABAMENTO:
I - TIPO 2B ATÉ O VISOR
TIPO 2A ACIMA DO VISOR
II - TIPO 2B ATÉ 0,70m
TIPO 1 DE 0,72m A 1,92m
TIPO 2A ACIMA DE 1,94m
III - TIPO 2B ATÉ 0,92m
TIPO 1 DE 0,94m A 1,84m
TIPO 2A DE 1,86m
TIPOS 1, 2A E 2B: V. ESTÚDIO B

 sólido do valle		
ESTÚDIO DA MONTANHA		
DATA: 10/05/07	ESTÚDIO C TRATAMENTO ACÚSTICO	VERSÃO: 1.0
ESCALA: 1:20	PAREDES E TETO LOCALIZAÇÃO DE TIPOS	PROJETO: 