

LEGENDA:

== existente aprovado / Processo nº 07757/91
==acrécimo

LEGENDA:

PORTAS

P1 = 0.60 x 2.10

P2 = 0.70 x 2.10

P3 = 0.80 x 2.10

P4 = 0.90 x 2.10

P5 = 1.00 x 2.10

P6 = 1.10 x 2.10

P7 = 1.20 x 2.10

Prefeitura Municipal de Nova Friburgo
Secretaria do Meio Ambiente
DEFERIDO
Processo nº 01631/08
Nova Friburgo, 29 de agosto de 2008
Arquit. Roberto de Gouveia Vianna Secretário do Meio Ambiente

PROJETO PARA LEGALIZAÇÃO DE ACRÉSCIMO DE
UMA CONSTRUÇÃO DESTINADA A UM SPA, SITO A
RUA VIRGINIA RIBEIRO, Nº 1865, PARQUE WALTER
ZABEL, ALTO 50,

MURY — NOVA FRIBURGO — RJ.

Proprietário Shami Gur
Arquiteta Participações Ltda.
Suzanne Perry


Projeto Rogério Nogueira Kato — CREA 33185 D RJ
Resp. técnico Arquiteto

PLANTA BAIXA — 2º PAV.

data MARÇO — 2008	escala indicada	desenho em CAD Max Araujo
----------------------	--------------------	------------------------------

Obs.:

2/8

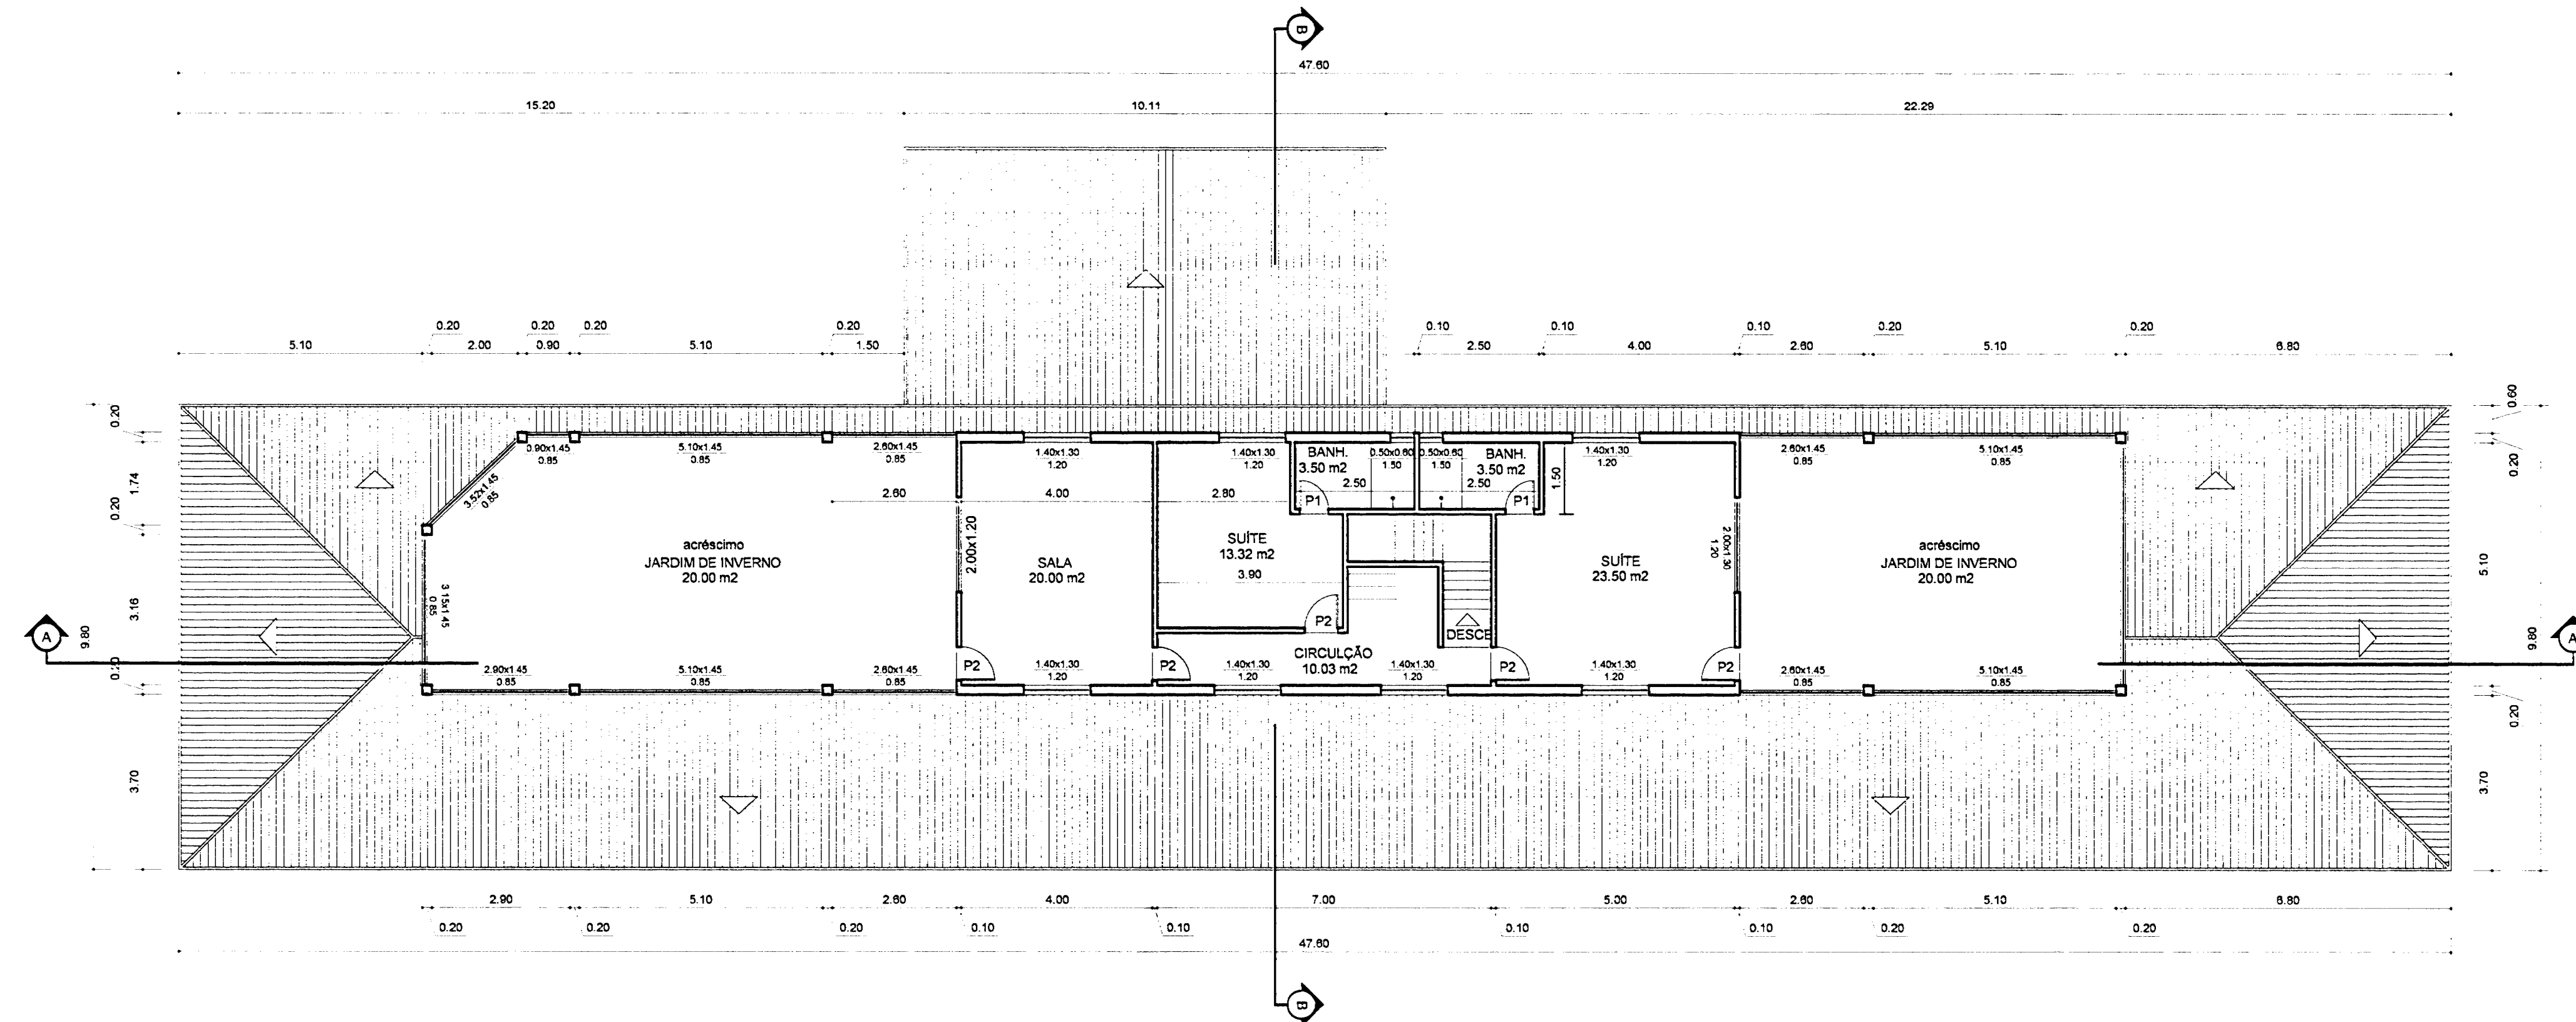

PLANTA BAIXA / 2º PAV.

ÁREA = 194.25 m²

ESCALA = 1/100