


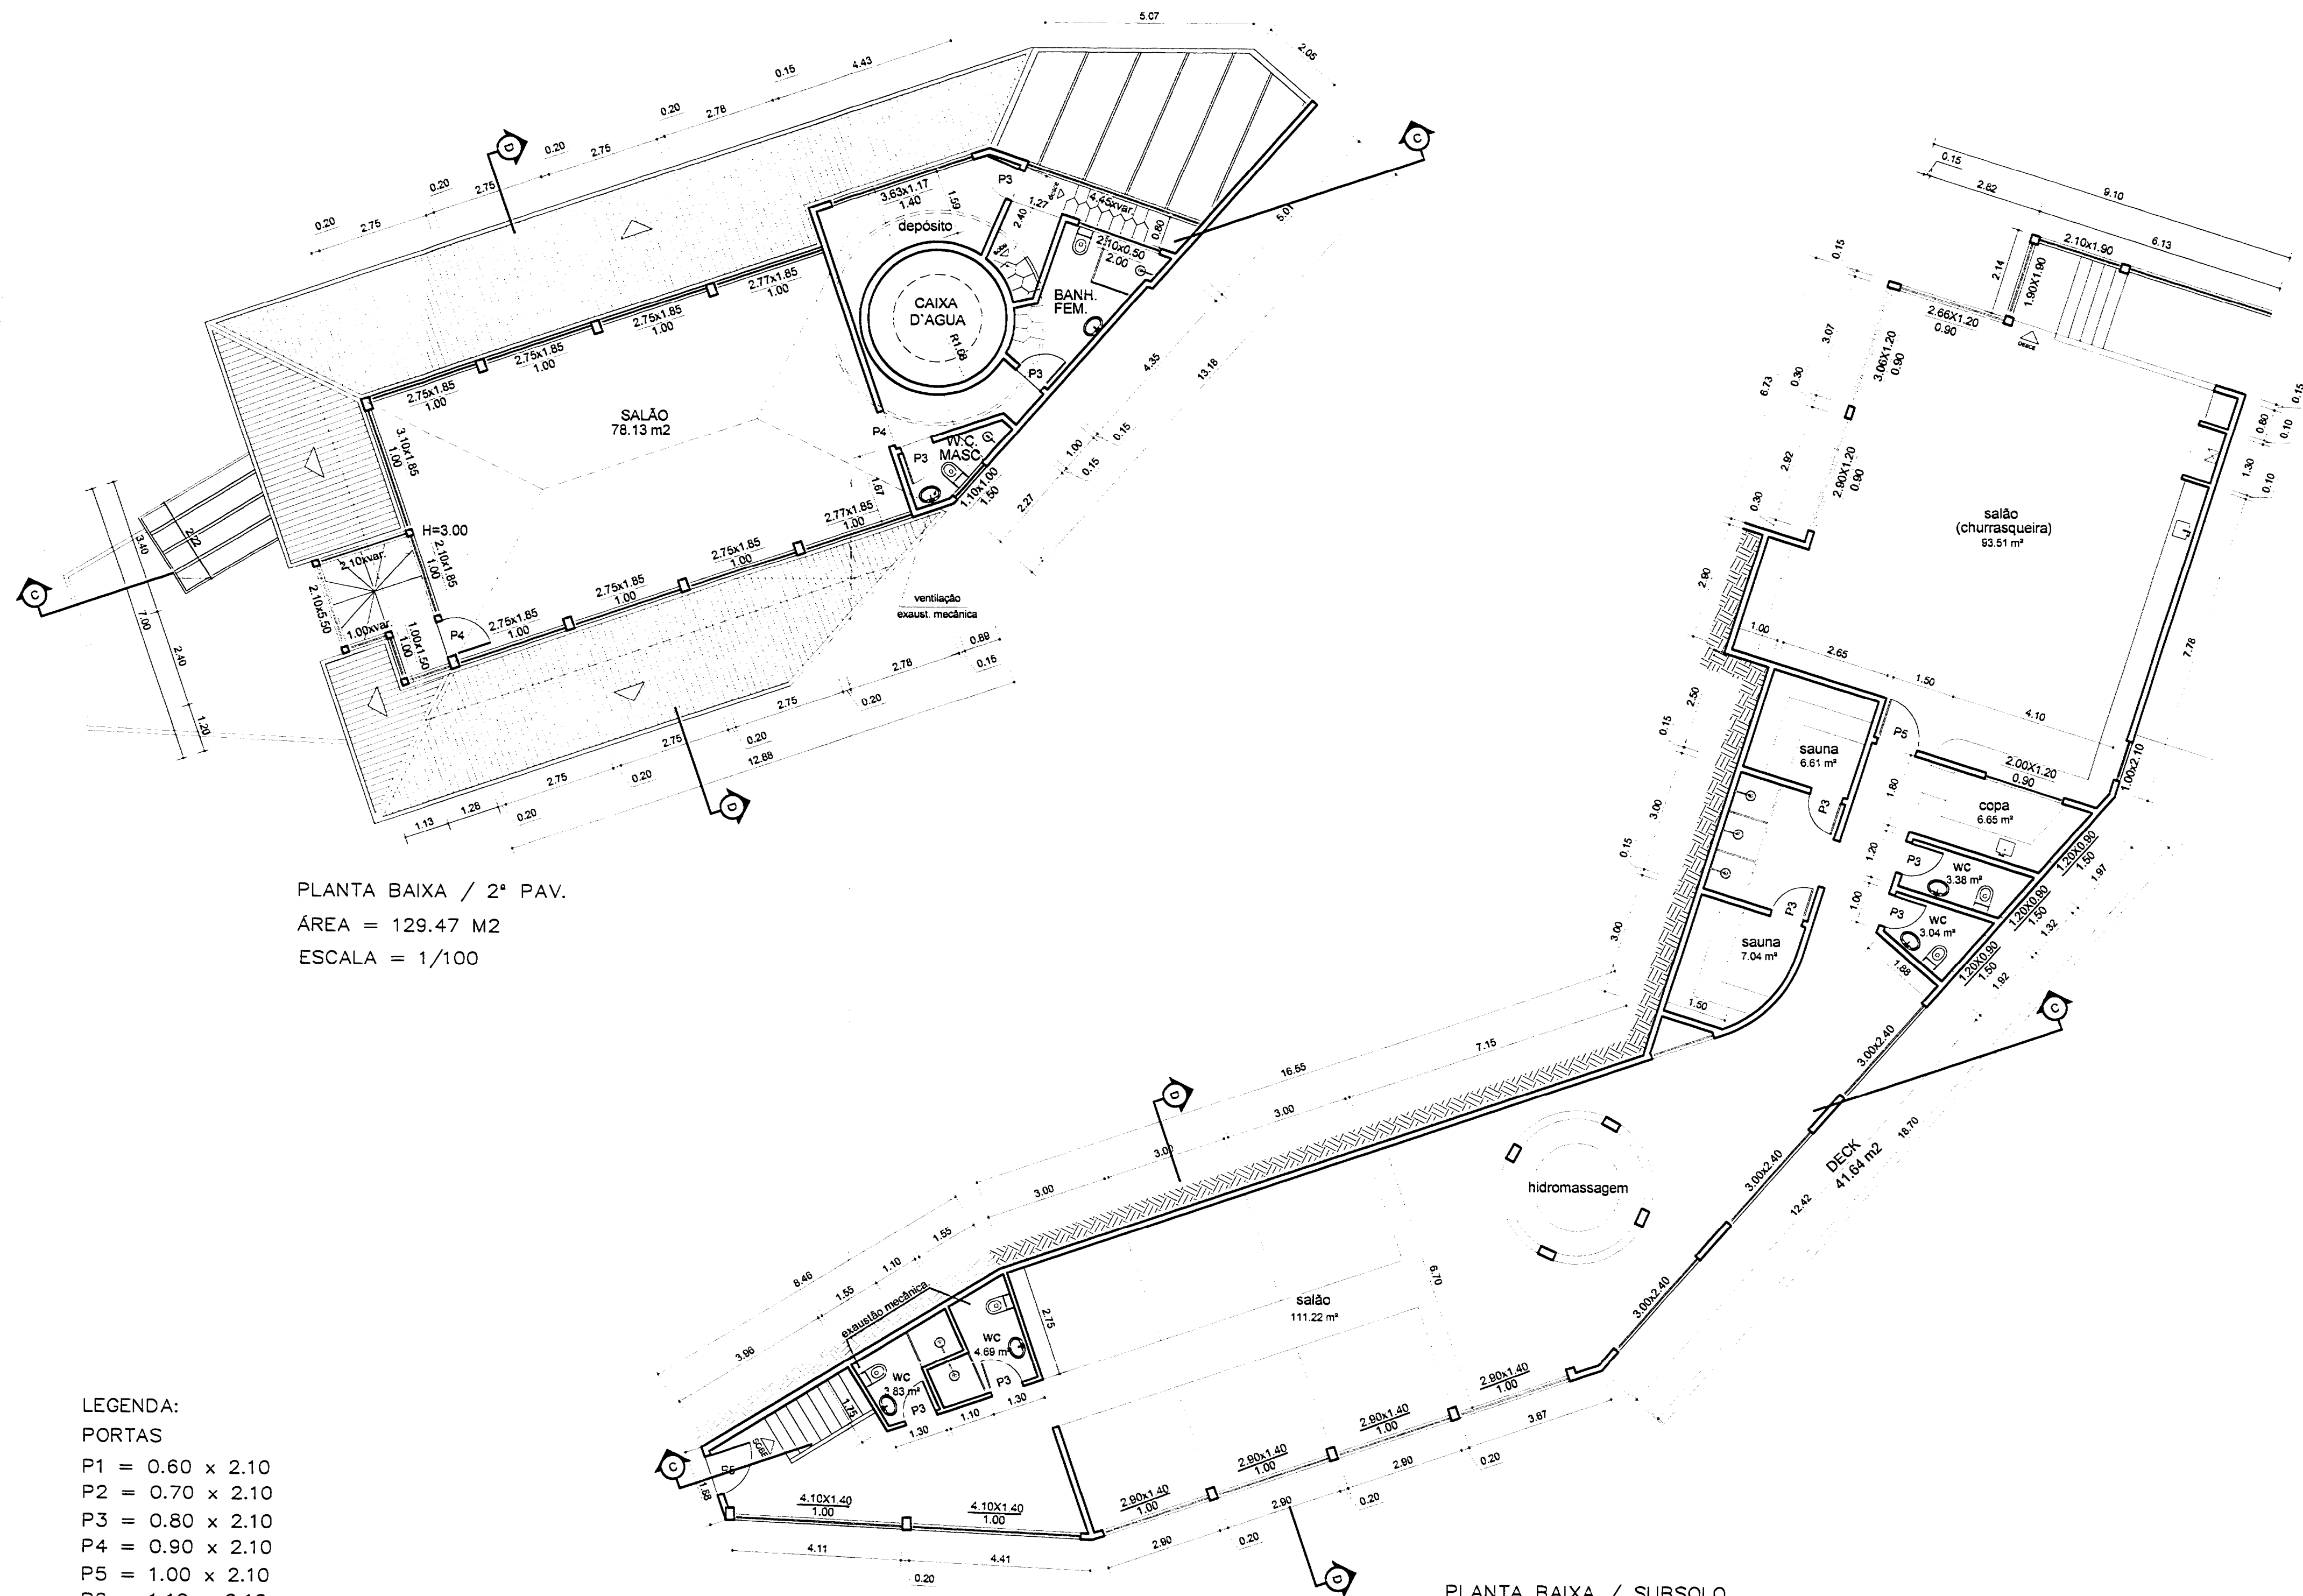

PLANTA BAIXA / 2º PAV.
ÁREA = 129.47 M2
ESCALA = 1/100

PLANTA BAIXA / SUBSOLO
ÁREA = 321.93 m2
ESCALA = 1/100

- LEGENDA:
PORTAS
P1 = 0.60 x 2.10
P2 = 0.70 x 2.10
P3 = 0.80 x 2.10
P4 = 0.90 x 2.10
P5 = 1.00 x 2.10
P6 = 1.10 x 2.10
P7 = 1.20 x 2.10

Prefeitura Municipal de Nova Friburgo
Secretaria do Meio Ambiente
DEFERIDO
Processo nº 4631/08
Nova Friburgo, 29 de agosto de 2008
Arquit. Roberto de Gouveia Vianna
Secretário do Meio Ambiente

PROJETO PARA LEGALIZAÇÃO DE ACRÉSCIMO DE
UMA CONSTRUÇÃO DESTINADA A UM SPA, SITO A
RUA VIRGINIA RIBEIRO, Nº 1865, PARQUE WALTER
ZABEL, ALTO 50,

MURY — NOVA FRIBURGO — RJ.

Proprietário Shami Gur
Arquiteta Participações Ltda.
Suzanne Perry

Projeto Rogério Nogueira Kato - OREA 33'85 D R
Resp. técnico Arquiteto

PLANTAS BAIXAS — SUBSOLO/2º PAV.

data MARÇO — 2008 escala indicada desenho em CAD Max Araujo

Obs.: Esta prancha só contém acréscimo