


CORTE AA
ESCALA = 1/100

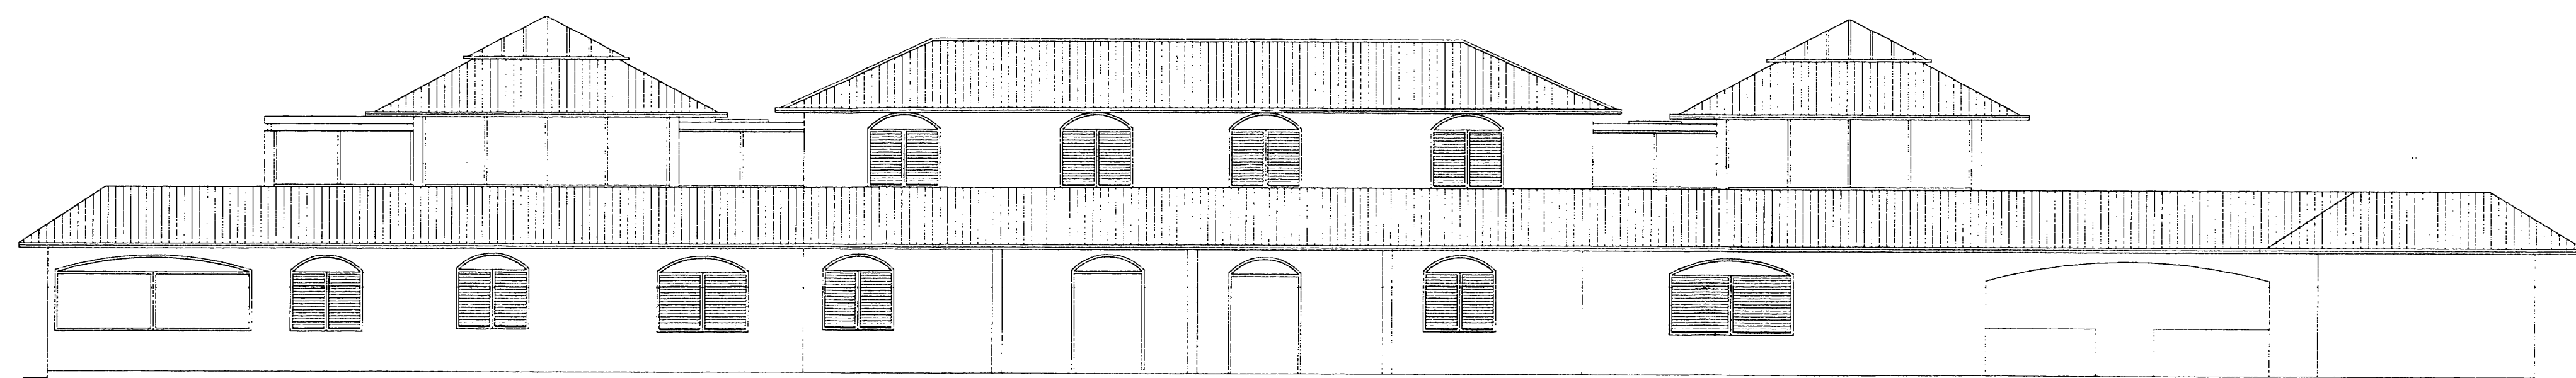


FACHADA CASA EXISTENTE
ESCALA = 1/100

LEGENDA:


PORTAS

- P1 = 0.60 x 2.10
- P2 = 0.70 x 2.10
- P3 = 0.80 x 2.10
- P4 = 0.90 x 2.10
- P5 = 1.00 x 2.10
- P6 = 1.10 x 2.10
- P7 = 1.20 x 2.10

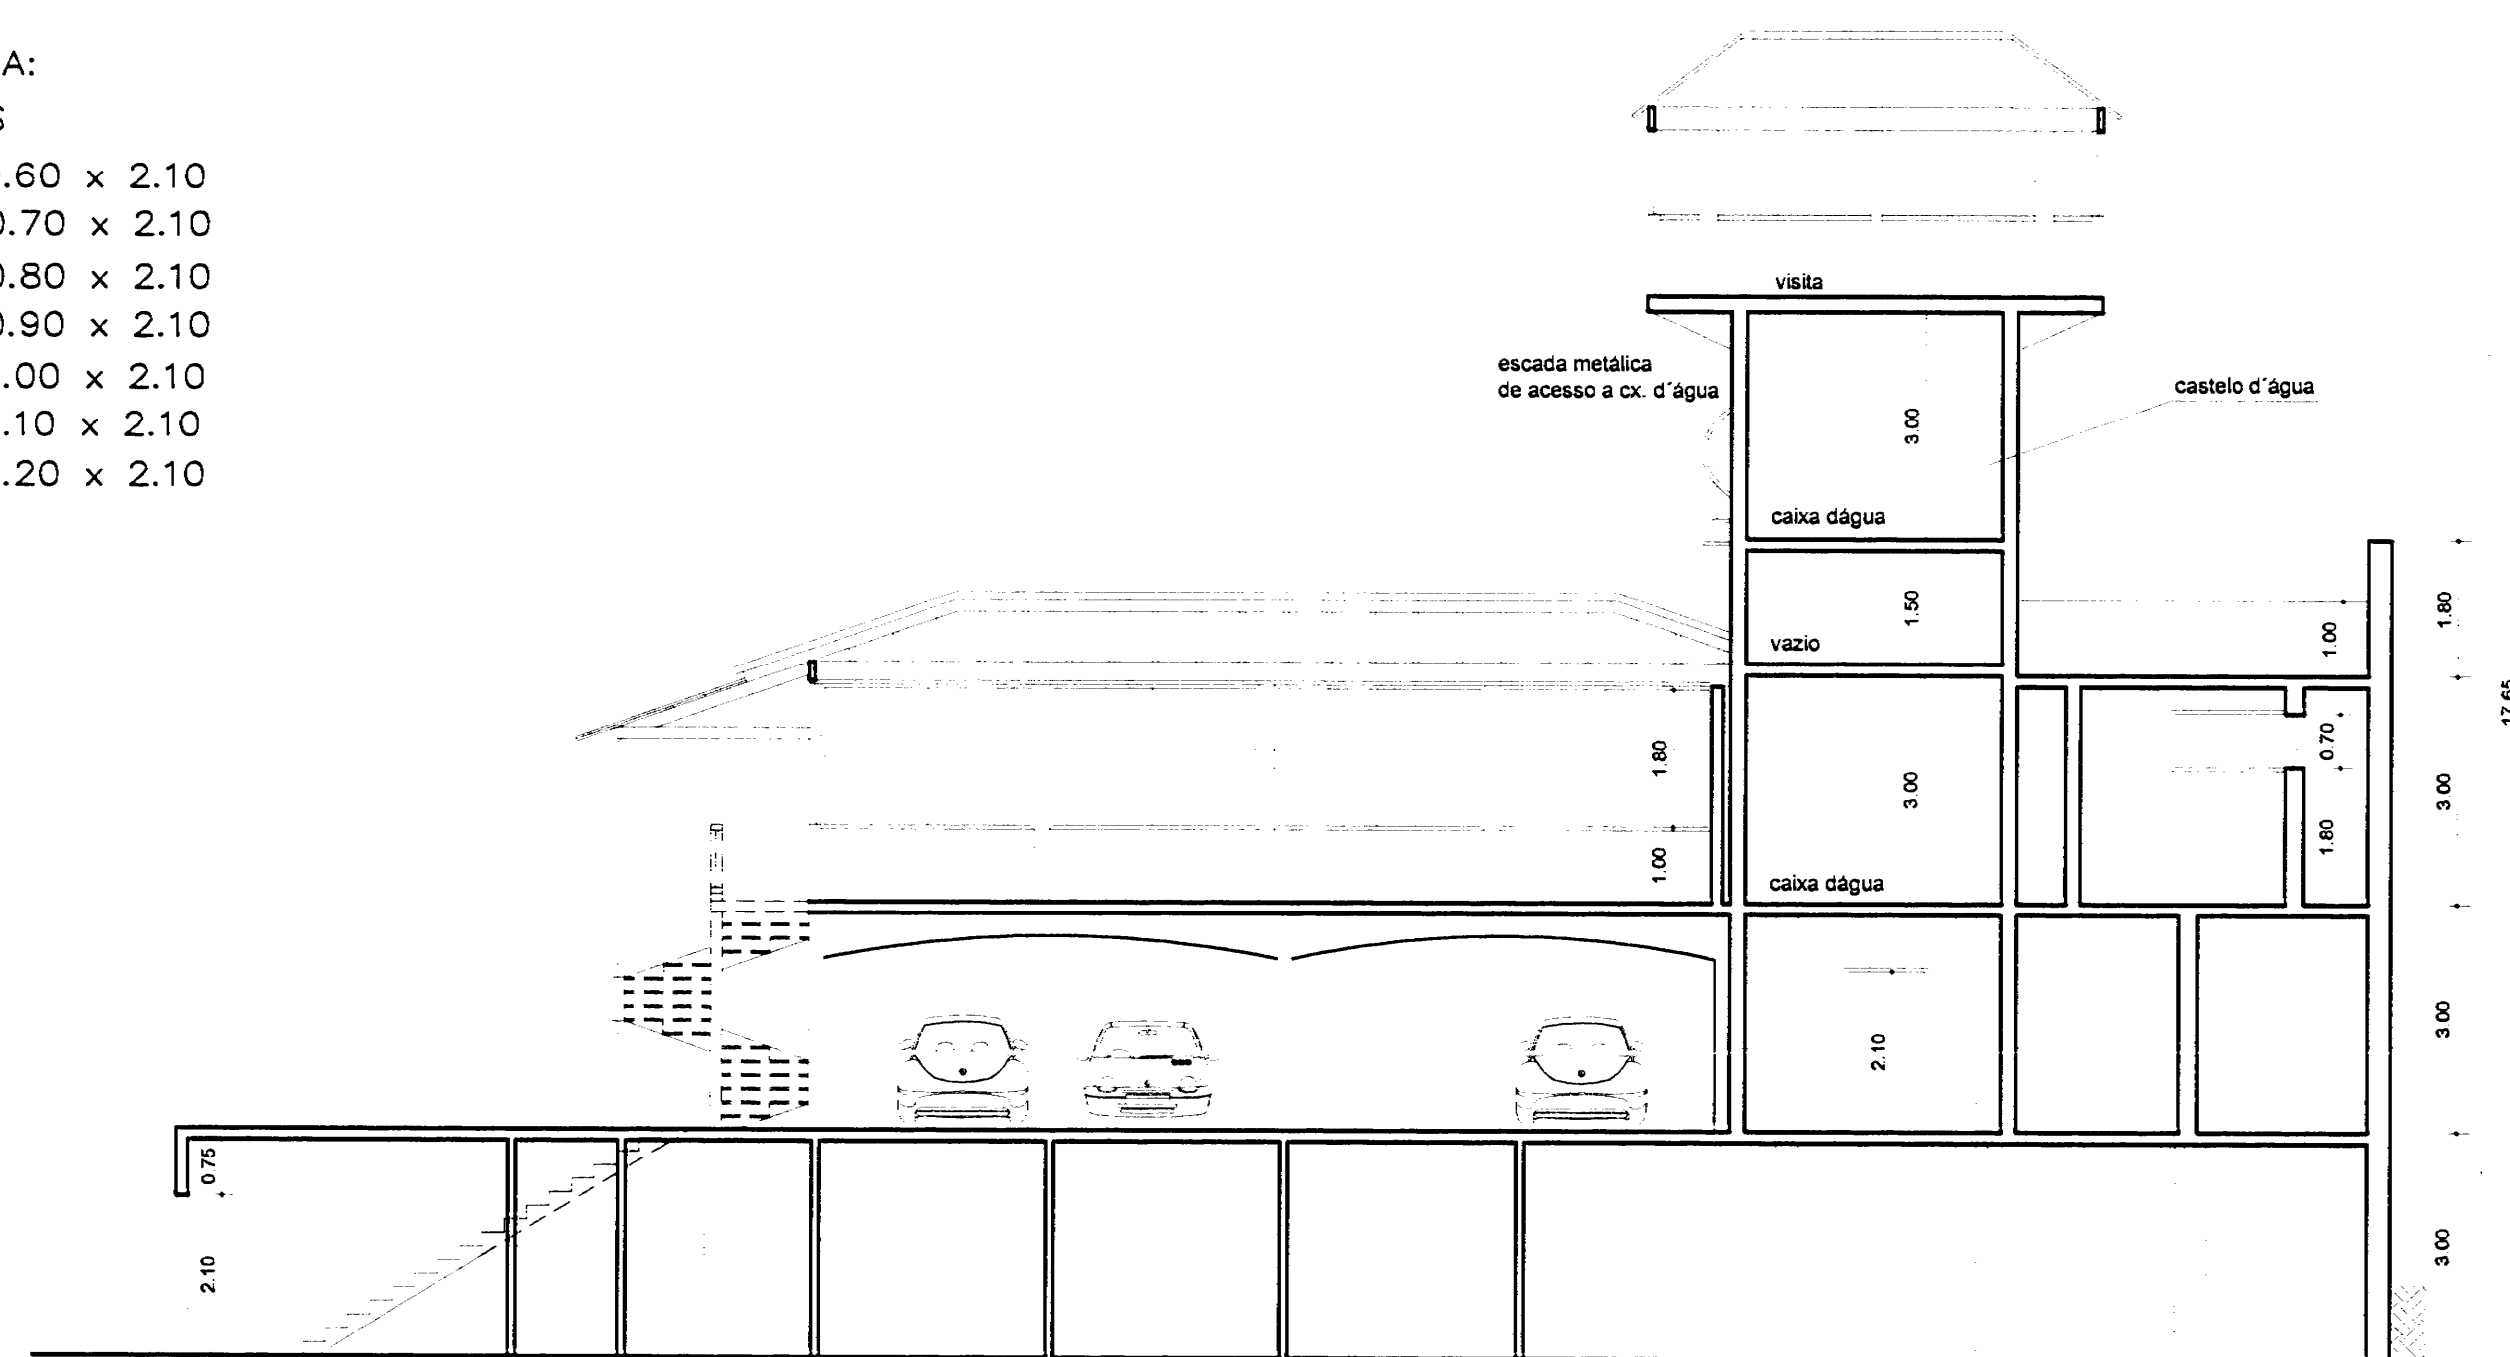


CORTE CC
ESCALA = 1/100


FACHADA/ GARAGEM
ESCALA = 1/100

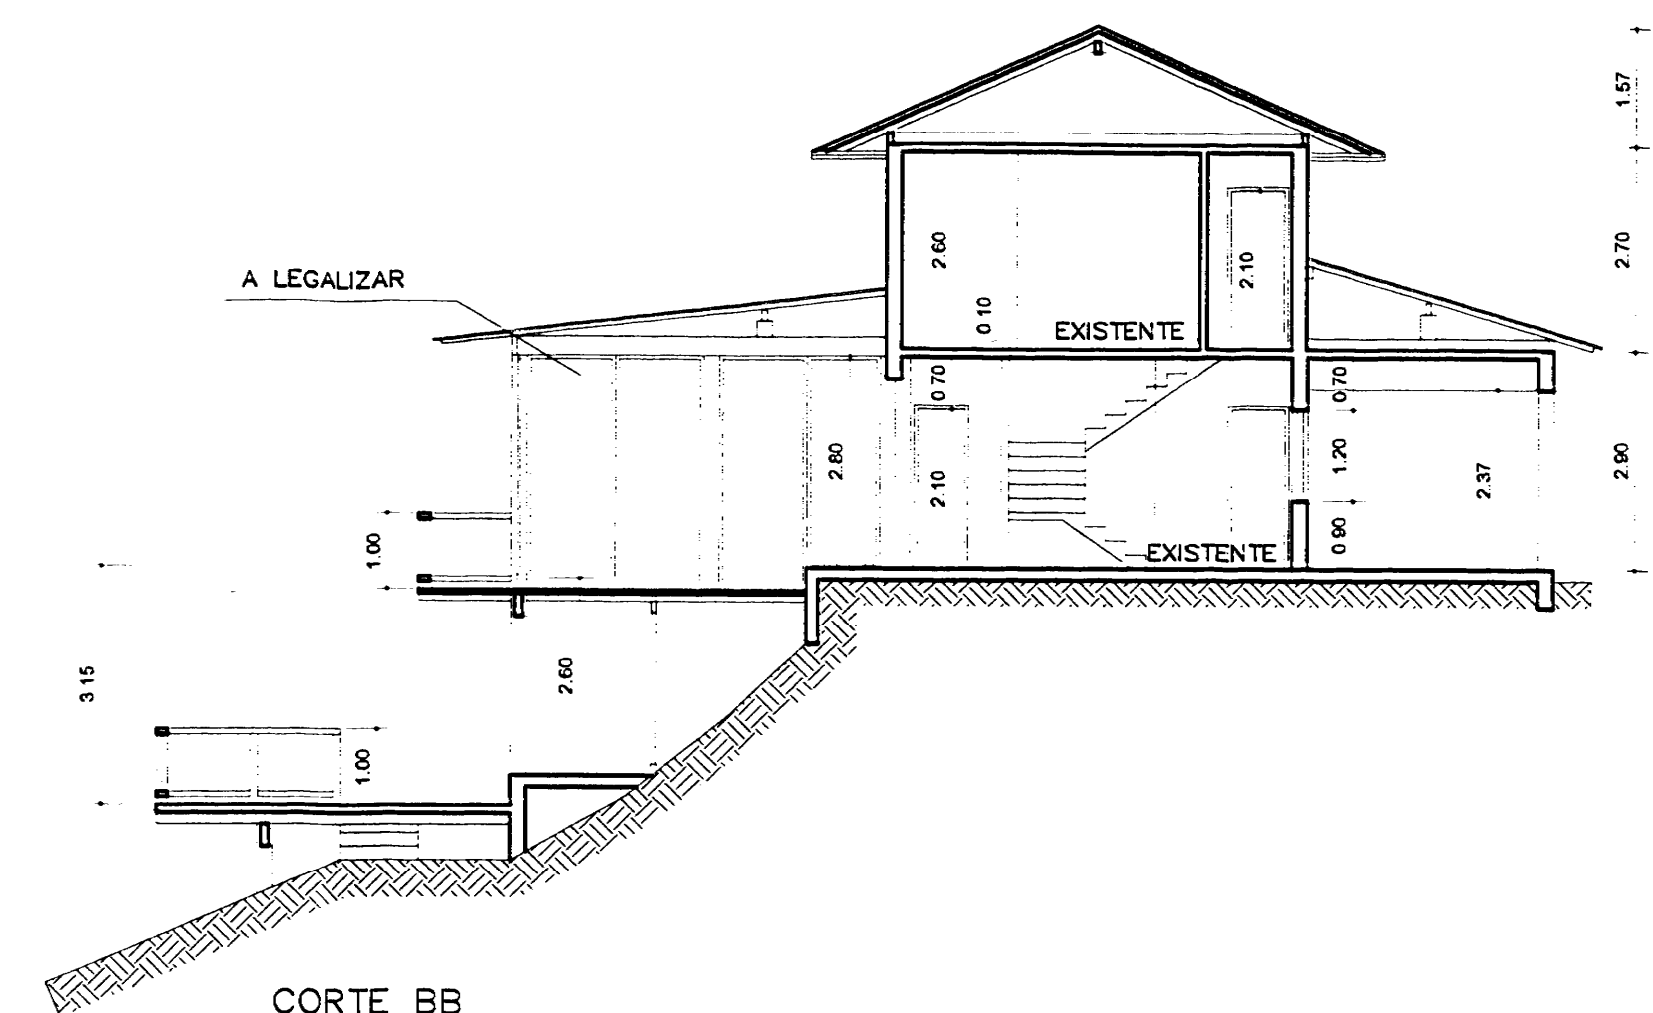

CORTE BB
ESCALA = 1/100

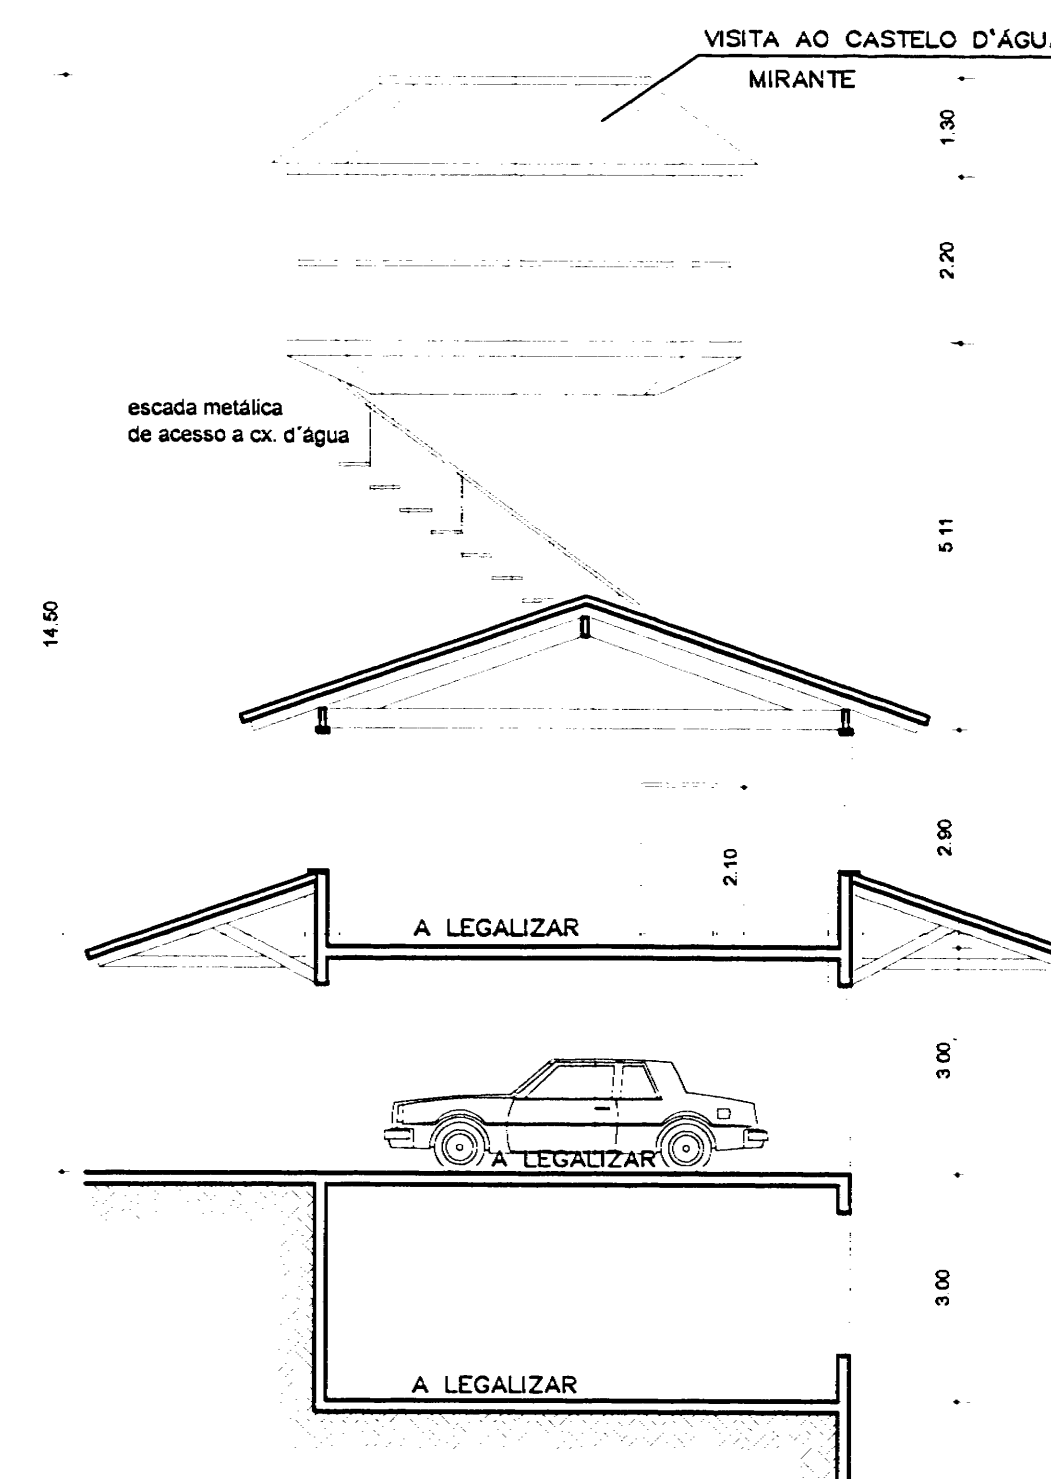

CORTE DD
ESCALA = 1/100

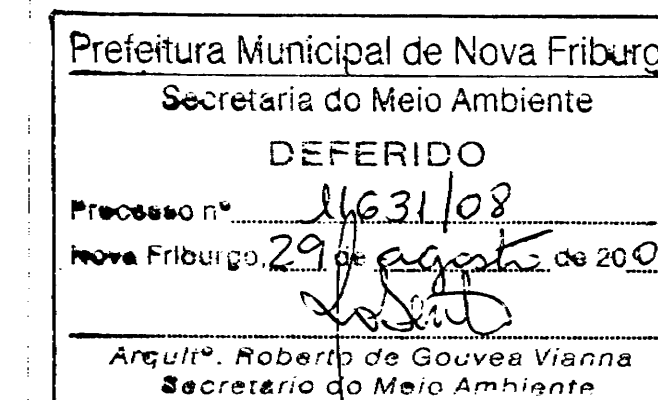

PROJETO PARA LEGALIZAÇÃO DE ACRÉSCIMO DE
UMA CONSTRUÇÃO DESTINADA A UM SPA, SITO A
RUA VIRGINIA RIBEIRO, N° 1865, PARQUE WALTER
ZABEL, ALTO 50,

MURY - NOVA FRIBURGO - RJ.

Proprietário: Shami Gur
Ametista Participações Ltda.

Projeto: Rogério Nogueira Kato - CREA 33185 D.R.
Resp. técnico: Arquiteto

CORTES E FACHADAS

data: MARÇO - 2008
escala: indicada
desenho em CAD: Max Araújo

Obs.: