

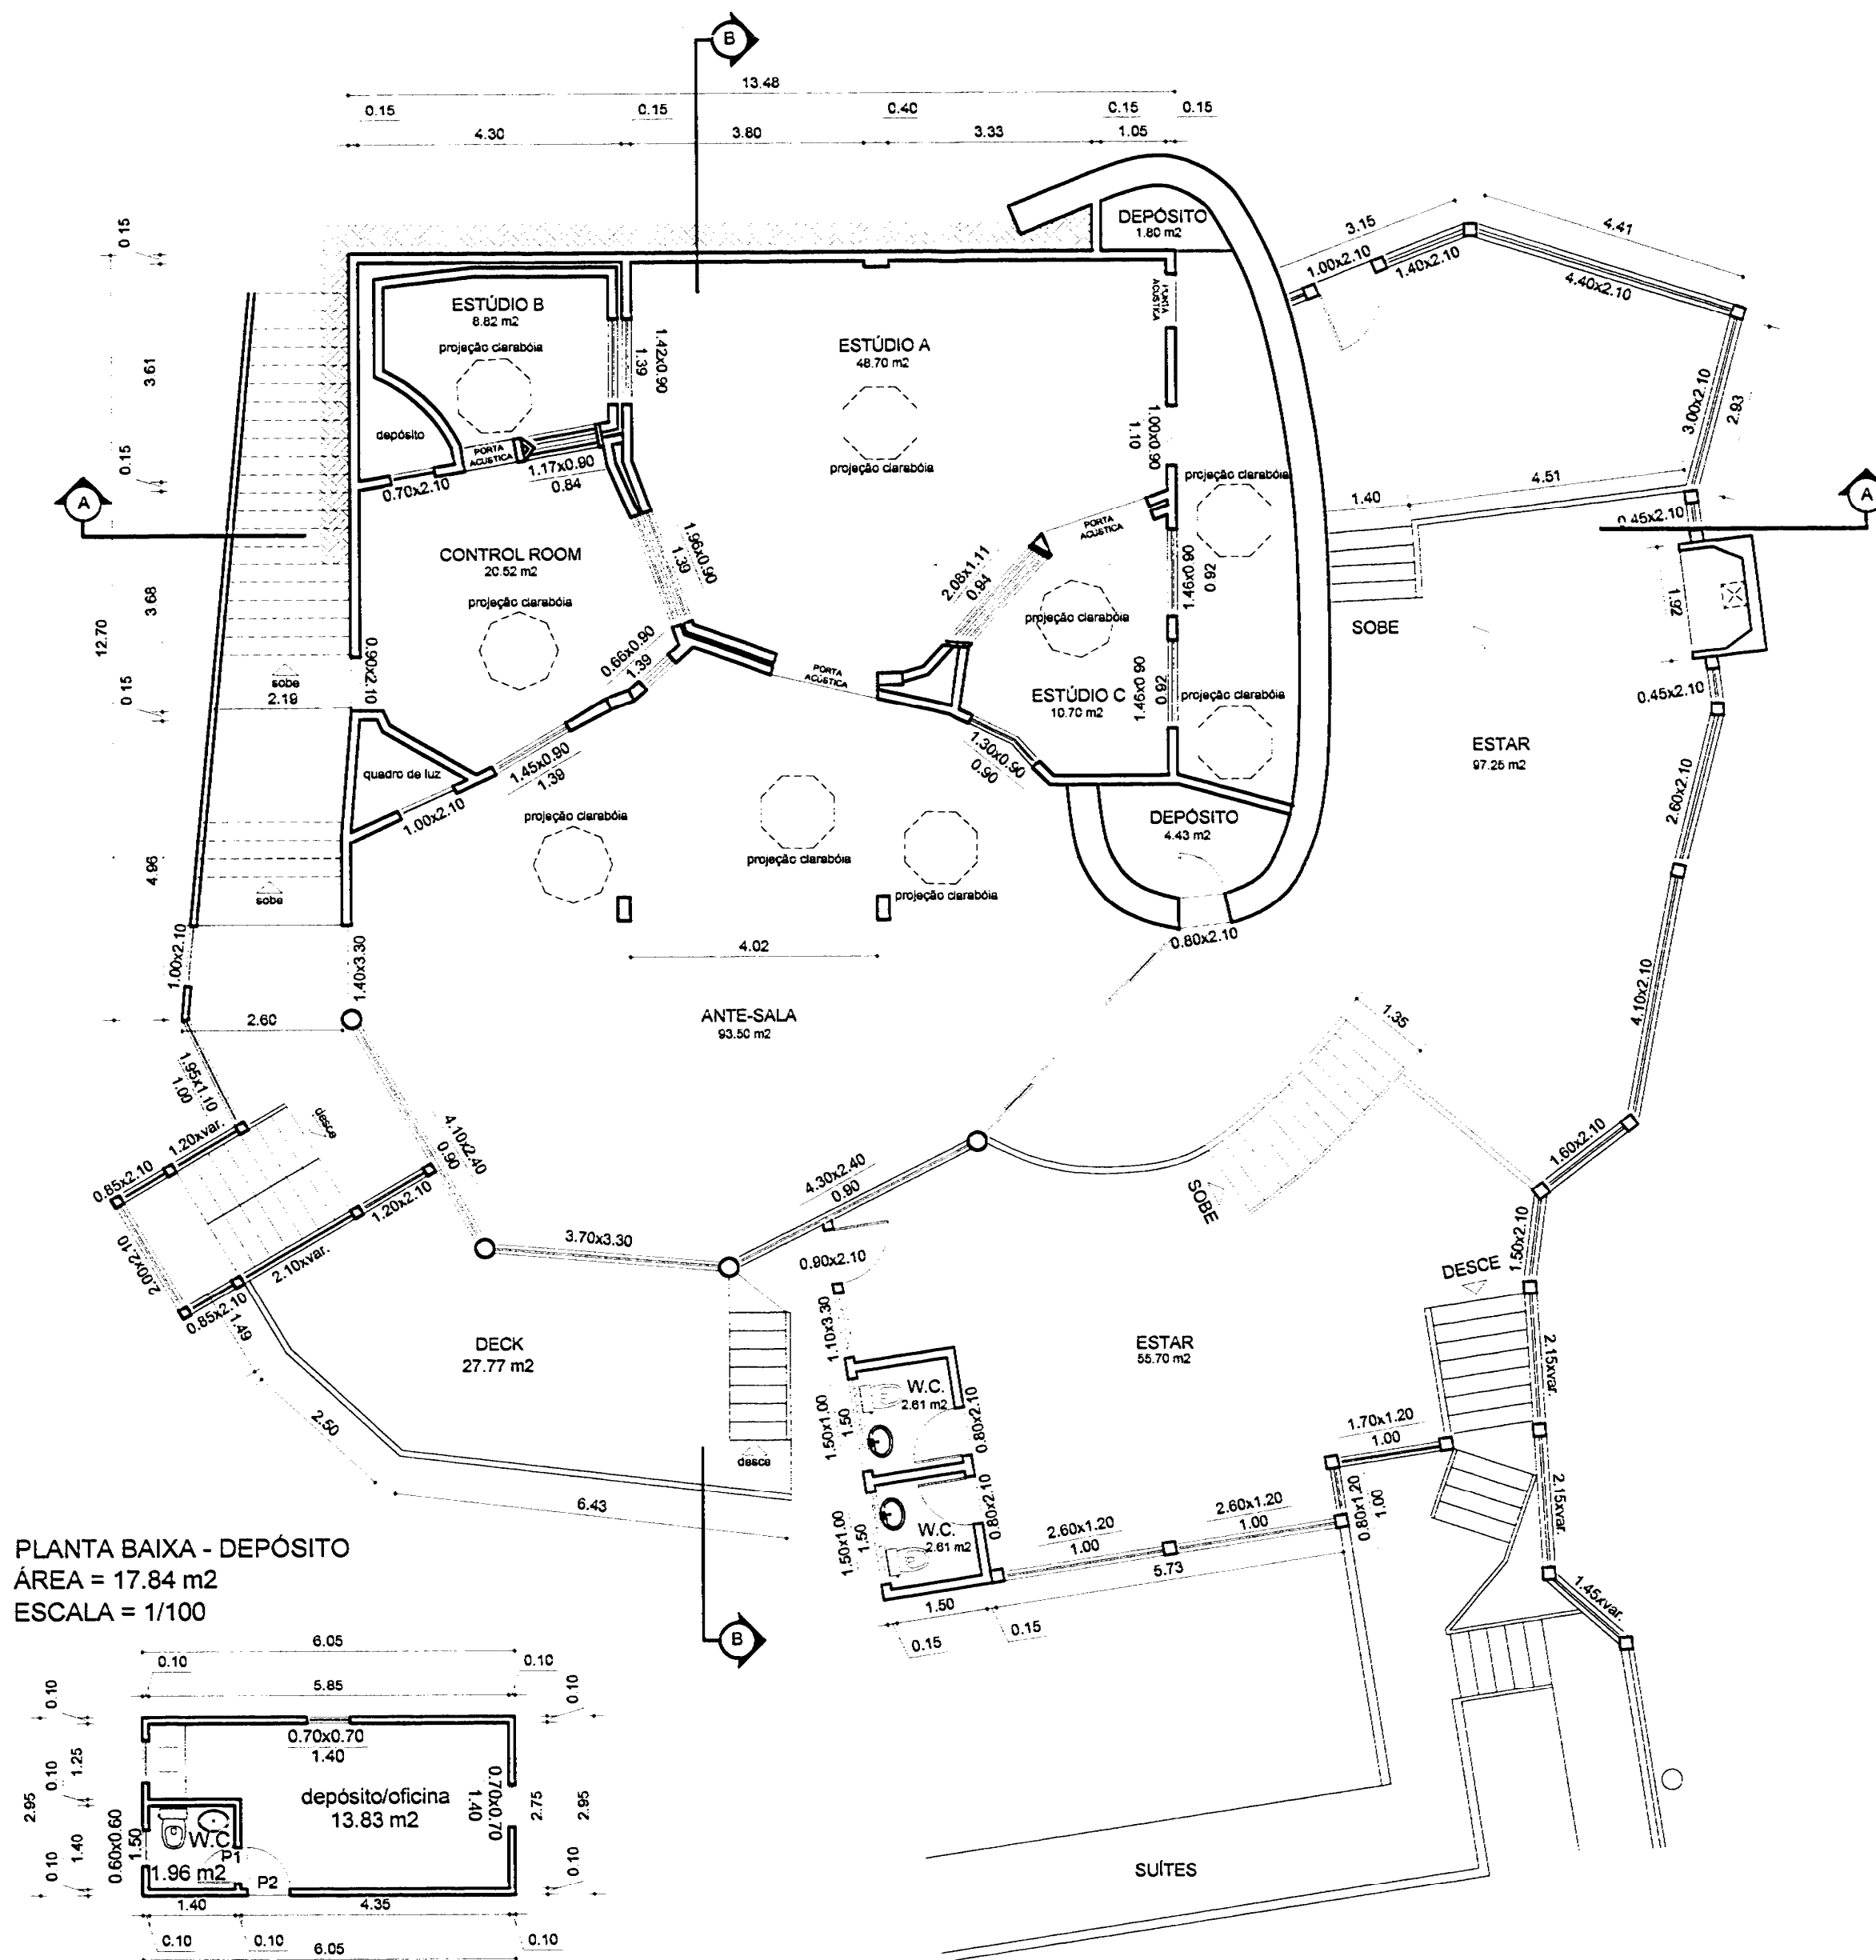


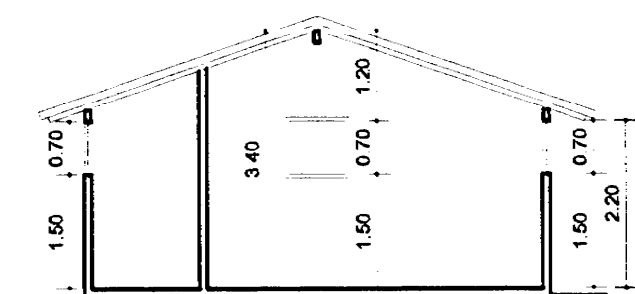

PLANTA BAIXA - DEPÓSITO
ÁREA = 17.84 m²
ESCALA = 1/100

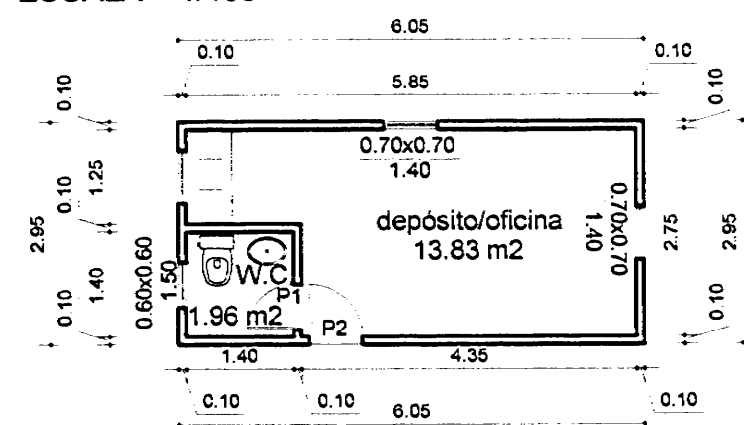

CORTE - DEPÓSITO
ESCALA = 1/100

PLANTA BAIXA - ESTÚDIO / ESTAR
ÁREA = 408.27 m²
ESCALA = 1/100

Prefeitura Municipal de Nova Friburgo
Secretaria do Meio Ambiente
DEFERIDO
Processo nº 11631/08
Nova Friburgo, 29 de agosto de 2008
Arquit. Roberto de Gouveia Vianna
Secretário do Meio Ambiente

PROJETO PARA LEGALIZAÇÃO DE ACRÉSCIMO DE
UMA CONSTRUÇÃO DESTINADA A UM SPA, SITO A
RUA VIRGINIA RIBEIRO, N° 1865, PARQUE WALTER
ZABEL, ALTO 50,

MURY - NOVA FRIBURGO - RJ.

Proprietário Shom' Gur
Suzanne Penny
Ametista Participações Ltda.

Projeto Rogério Nogueira Kato - CREA 33'85 D RJ
Resp. técnico Arquiteto

PLANTA BAIXA - ESTÚDIO / ESTAR / DEPÓSITO

data MARÇO - 2008 escala indicada desenho em CAD Max Araujo

Obs.: Esta plancha só contém acréscimo

5/8