



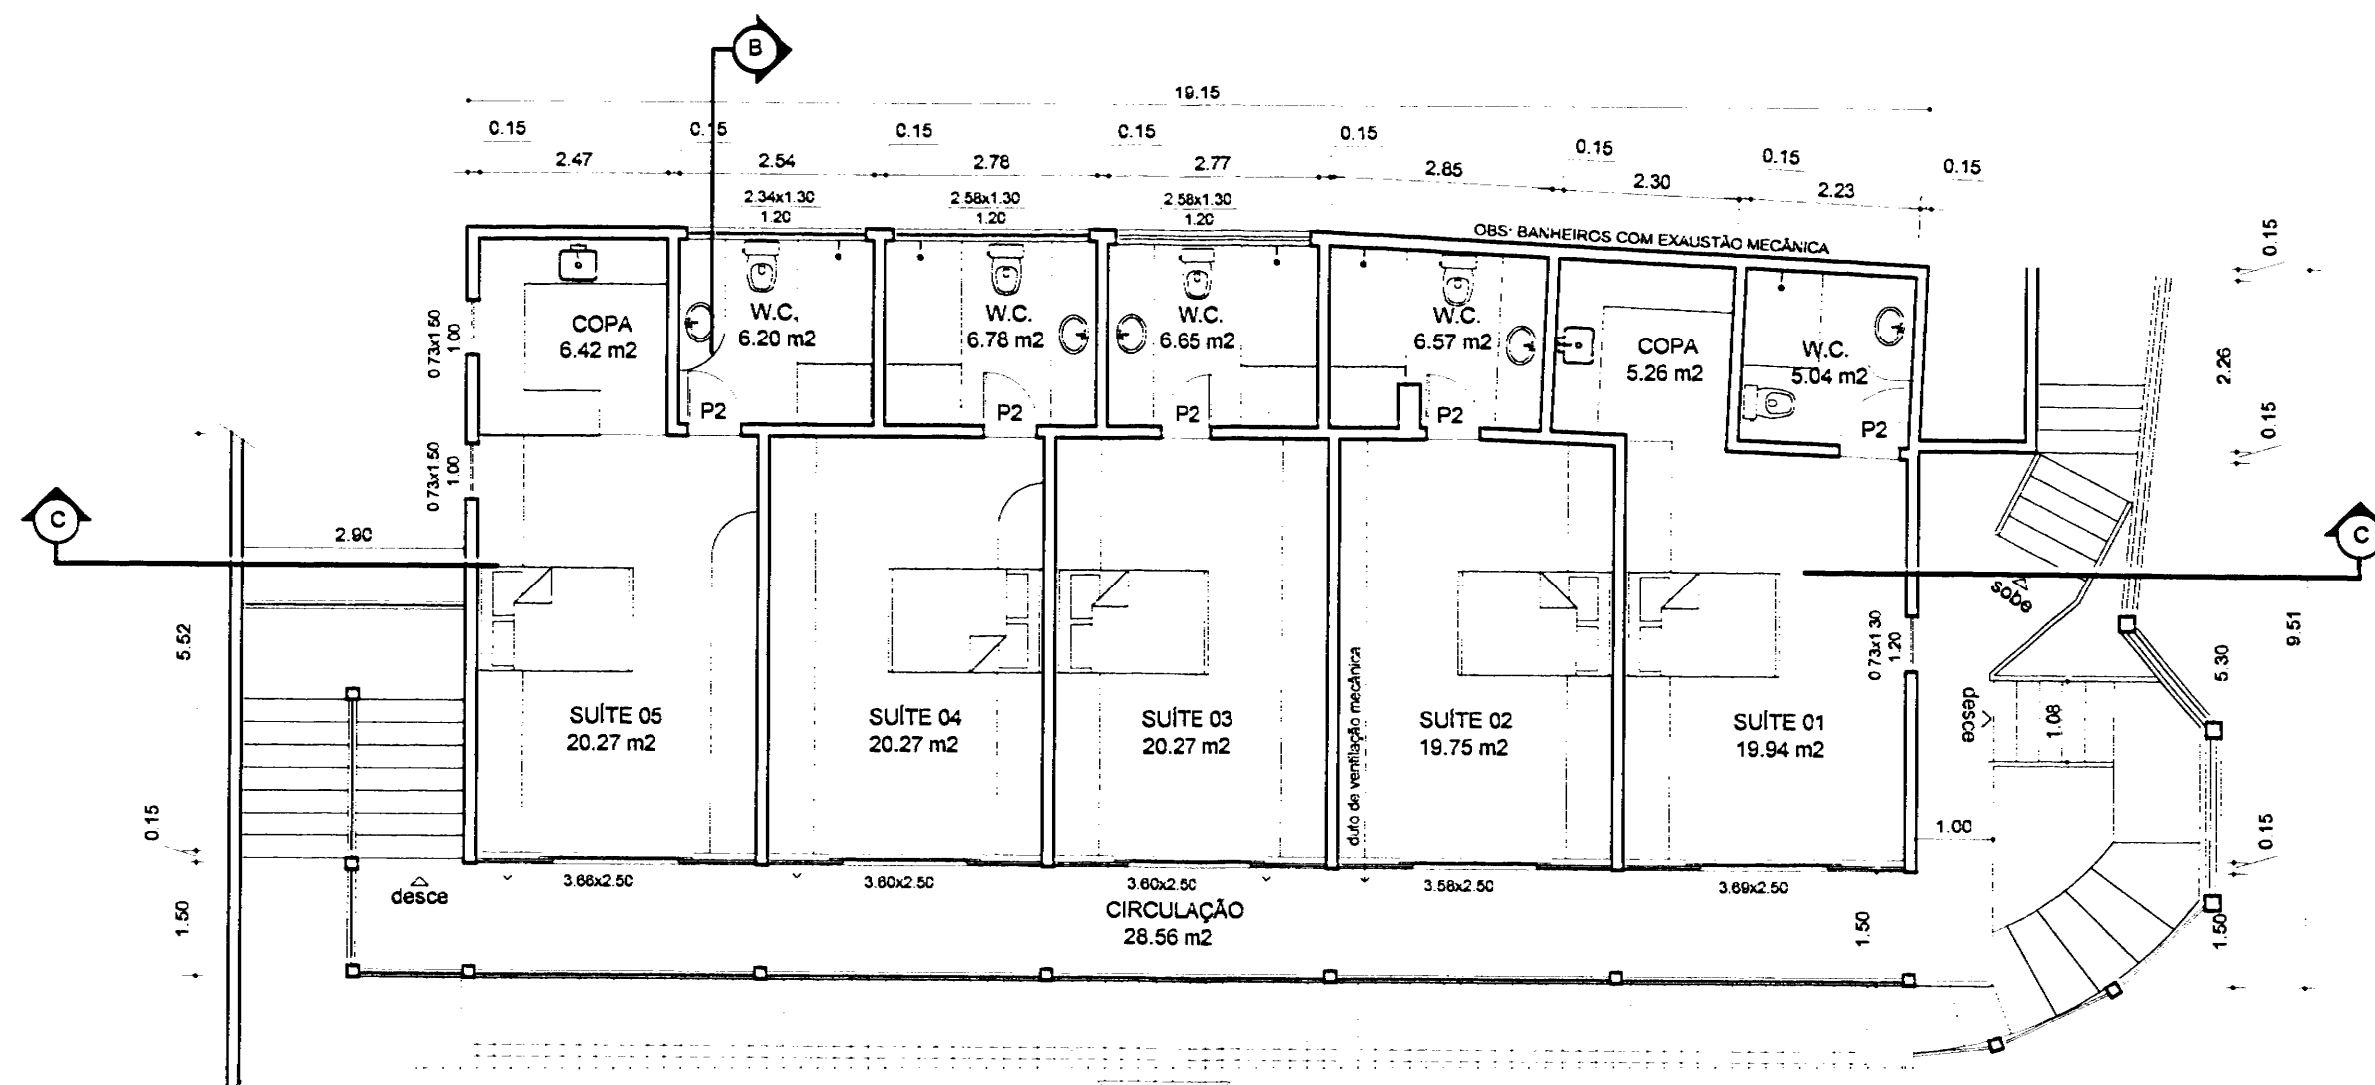

PLANTA BAIXA - SUÍTES / SUPERIOR
ÁREA = 195.00 m²
ESCALA = 1/100

- LEGENDA:
PORTAS
P1 = 0.60 x 2.10
P2 = 0.70 x 2.10
P3 = 0.80 x 2.10
P4 = 0.90 x 2.10
P5 = 1.00 x 2.10
P6 = 1.10 x 2.10
P7 = 1.20 x 2.10

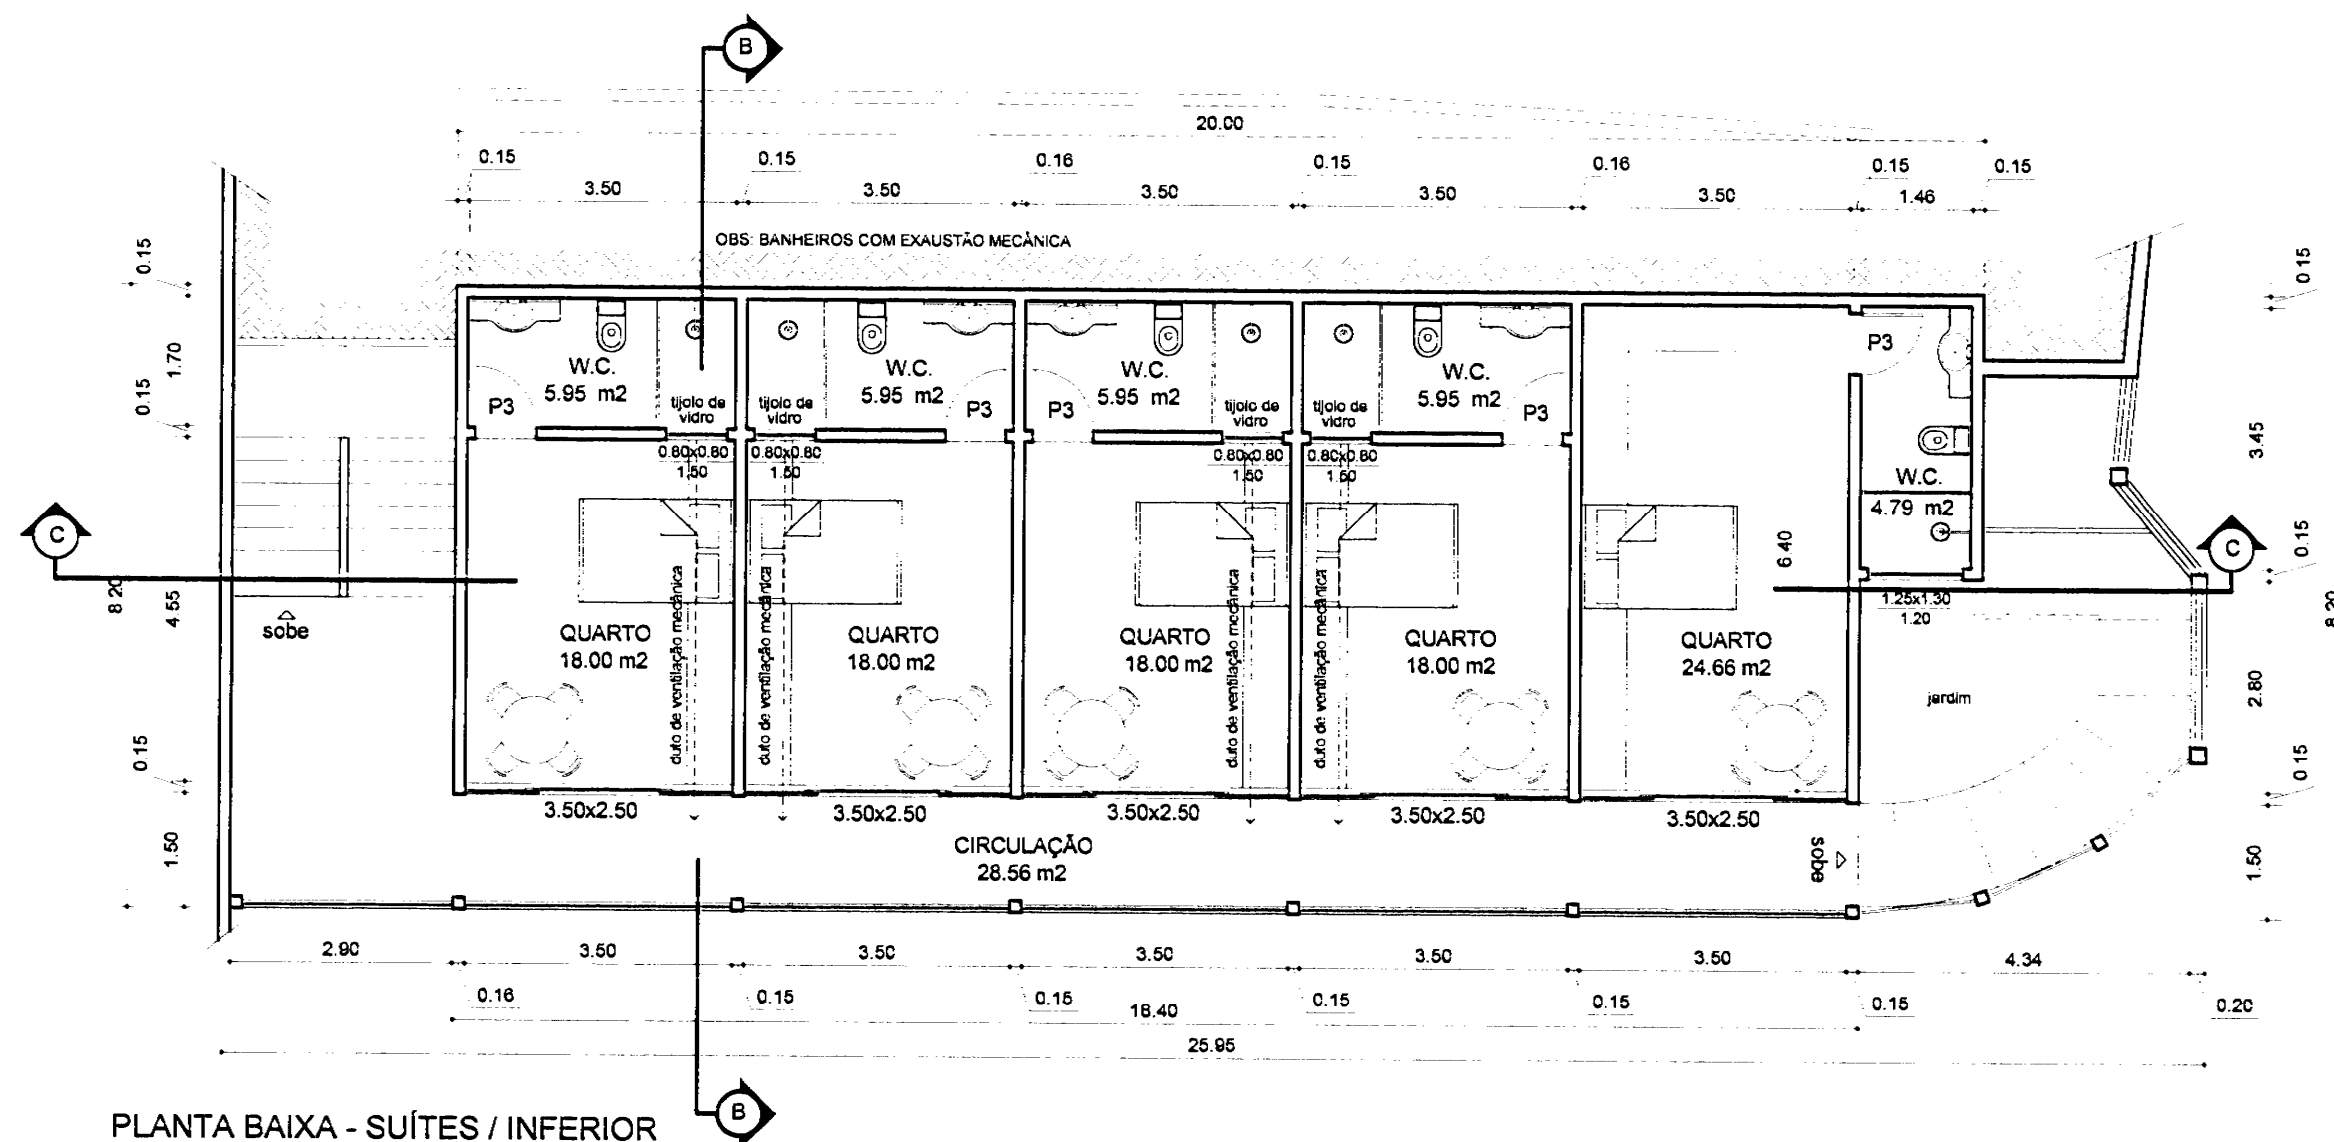

PLANTA BAIXA - SUÍTES / INFERIOR
ÁREA = 178.70 m²
ESCALA = 1/100

Prefeitura Municipal de Nova Friburgo
Secretaria do Meio Ambiente
DEFERIDO
Processo nº 11631/08
Nova Friburgo 29 de agosto de 2008
Arquit. Roberto de Gouveia Vianna
Secretário do Meio Ambiente

PROJETO PARA LEGALIZAÇÃO DE ACRÉSCIMO DE
UMA CONSTRUÇÃO DESTINADA A UM SPA, SITO A
RUA VIRGINIA RIBEIRO, Nº 1865, PARQUE WALTER
ZABEL, ALTO 50,

MURY — NOVA FRIBURGO — RJ.

Proprietário: Shami Gur, Suzzanne Penny, Ametista Participações Ltda.
Projeto: Rogério Nogueira Kato — CREA 33'85 D RJ
Resp. técnico: Arquiteto

PLANTAS BAIXAS — SUÍTES

data: MARÇO — 2008
escala: indicada
desenho em CAD: Max Araujo

Obs.: Esta prancha só contém acréscimo

6/8