




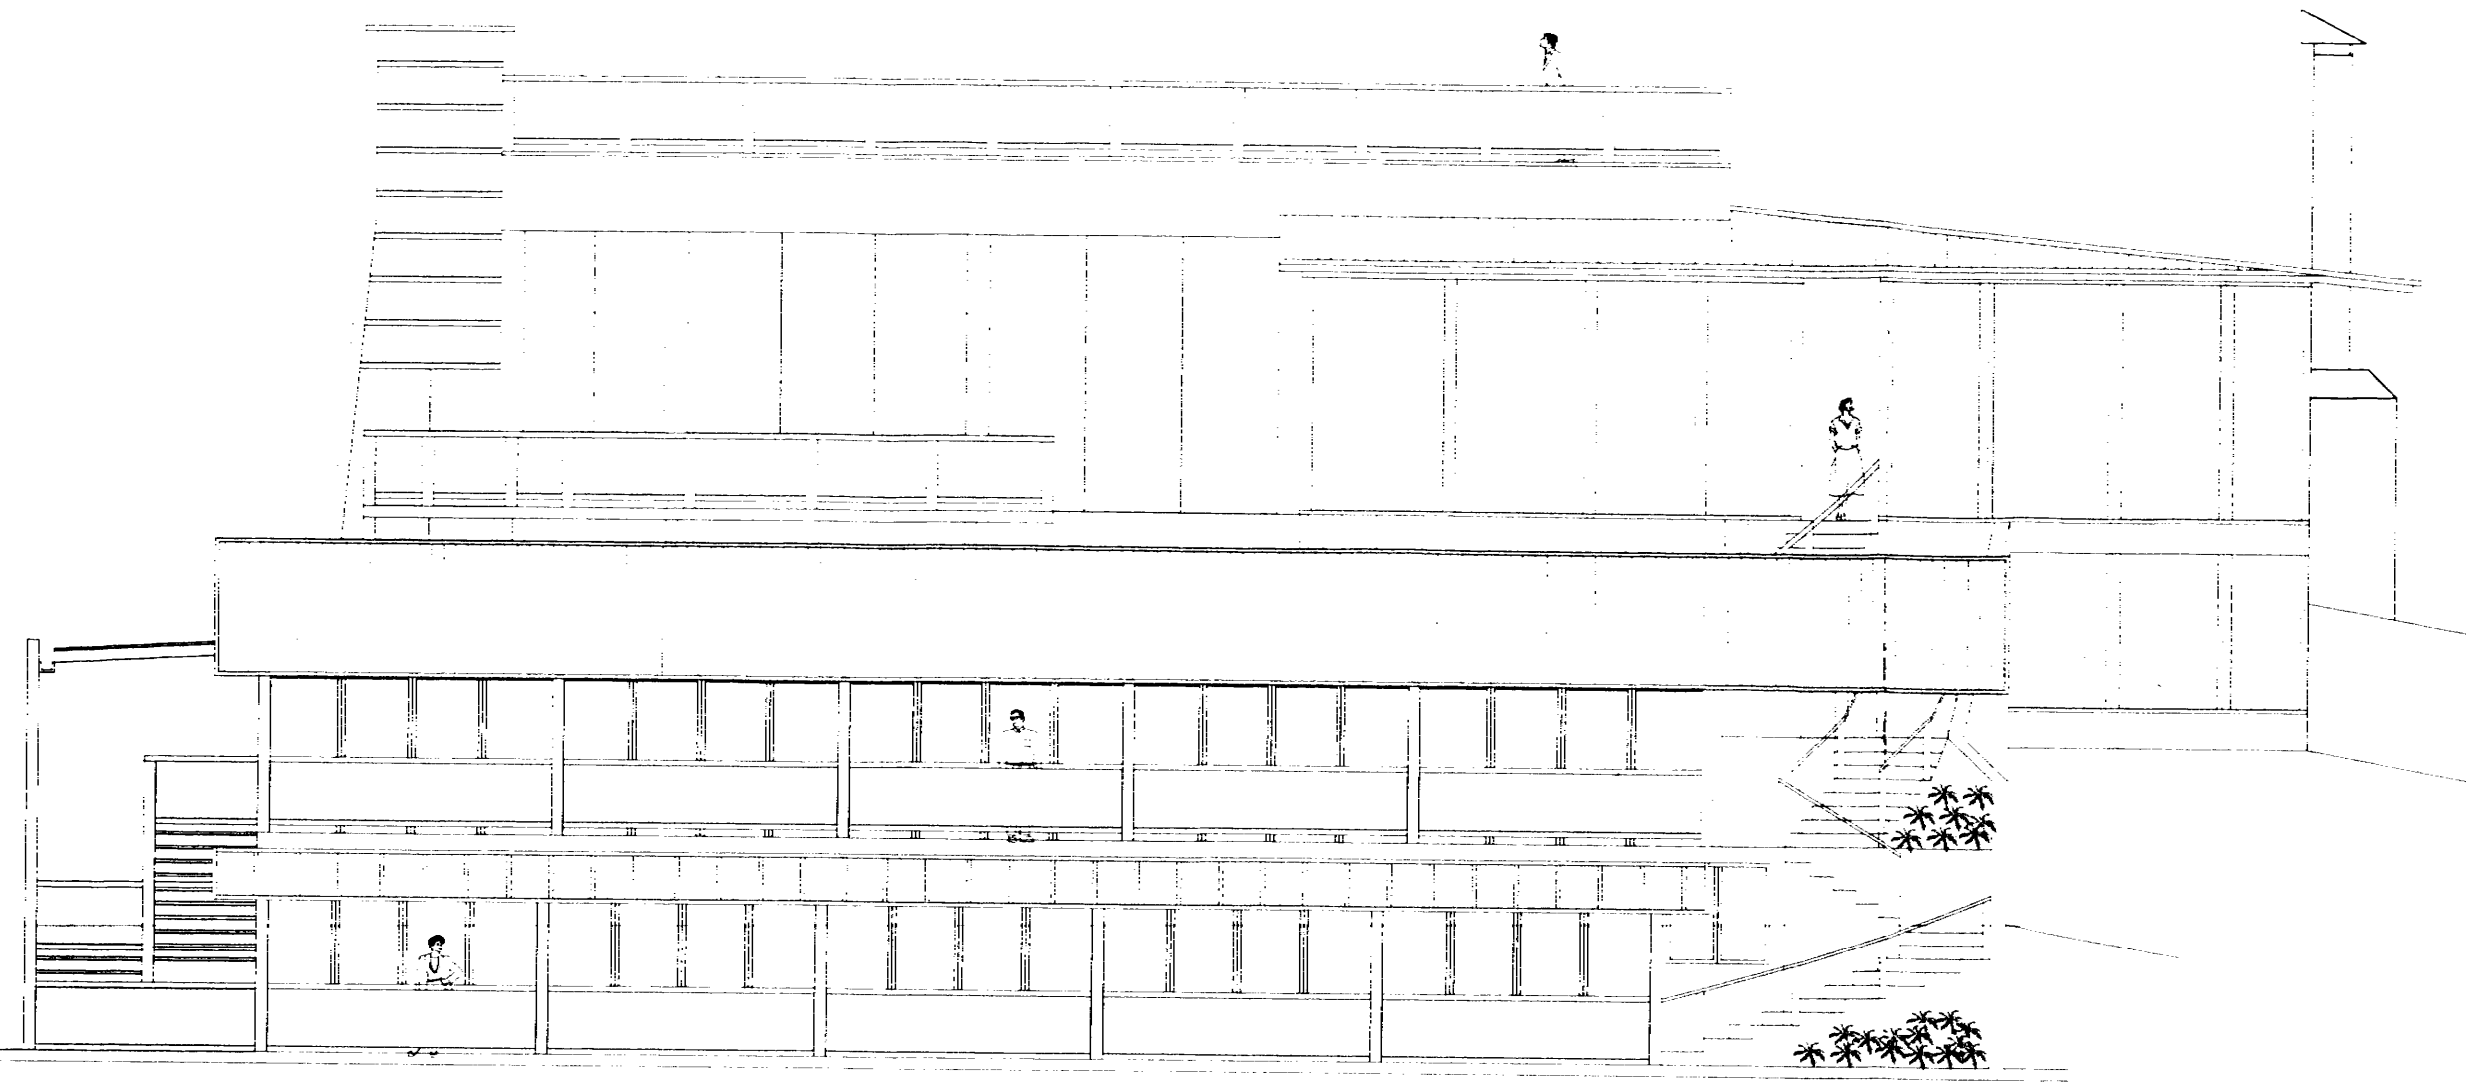


FACHADA
ESCALA = 1/200

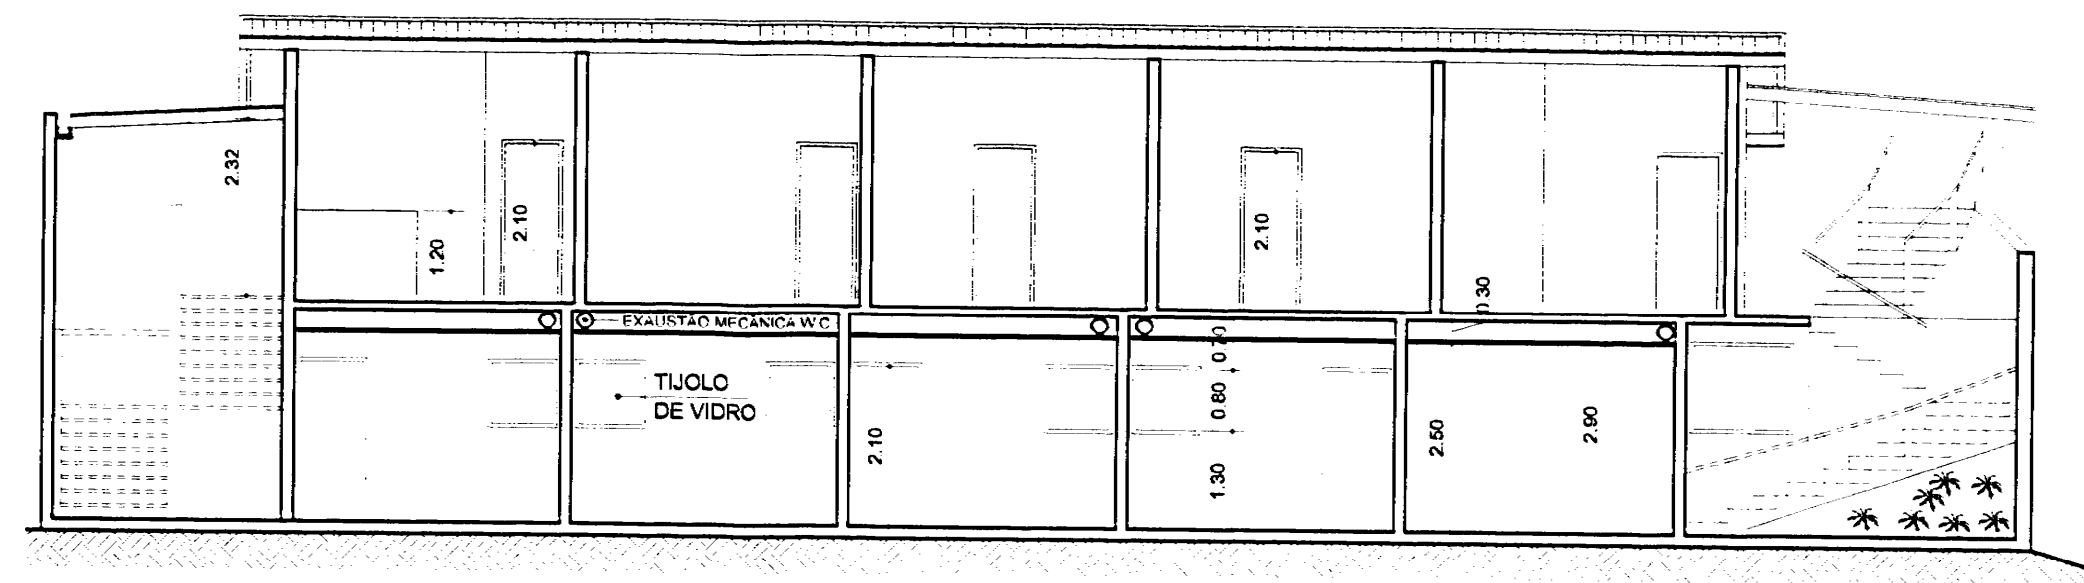

CORTE C-C
ESCALA = 1/100

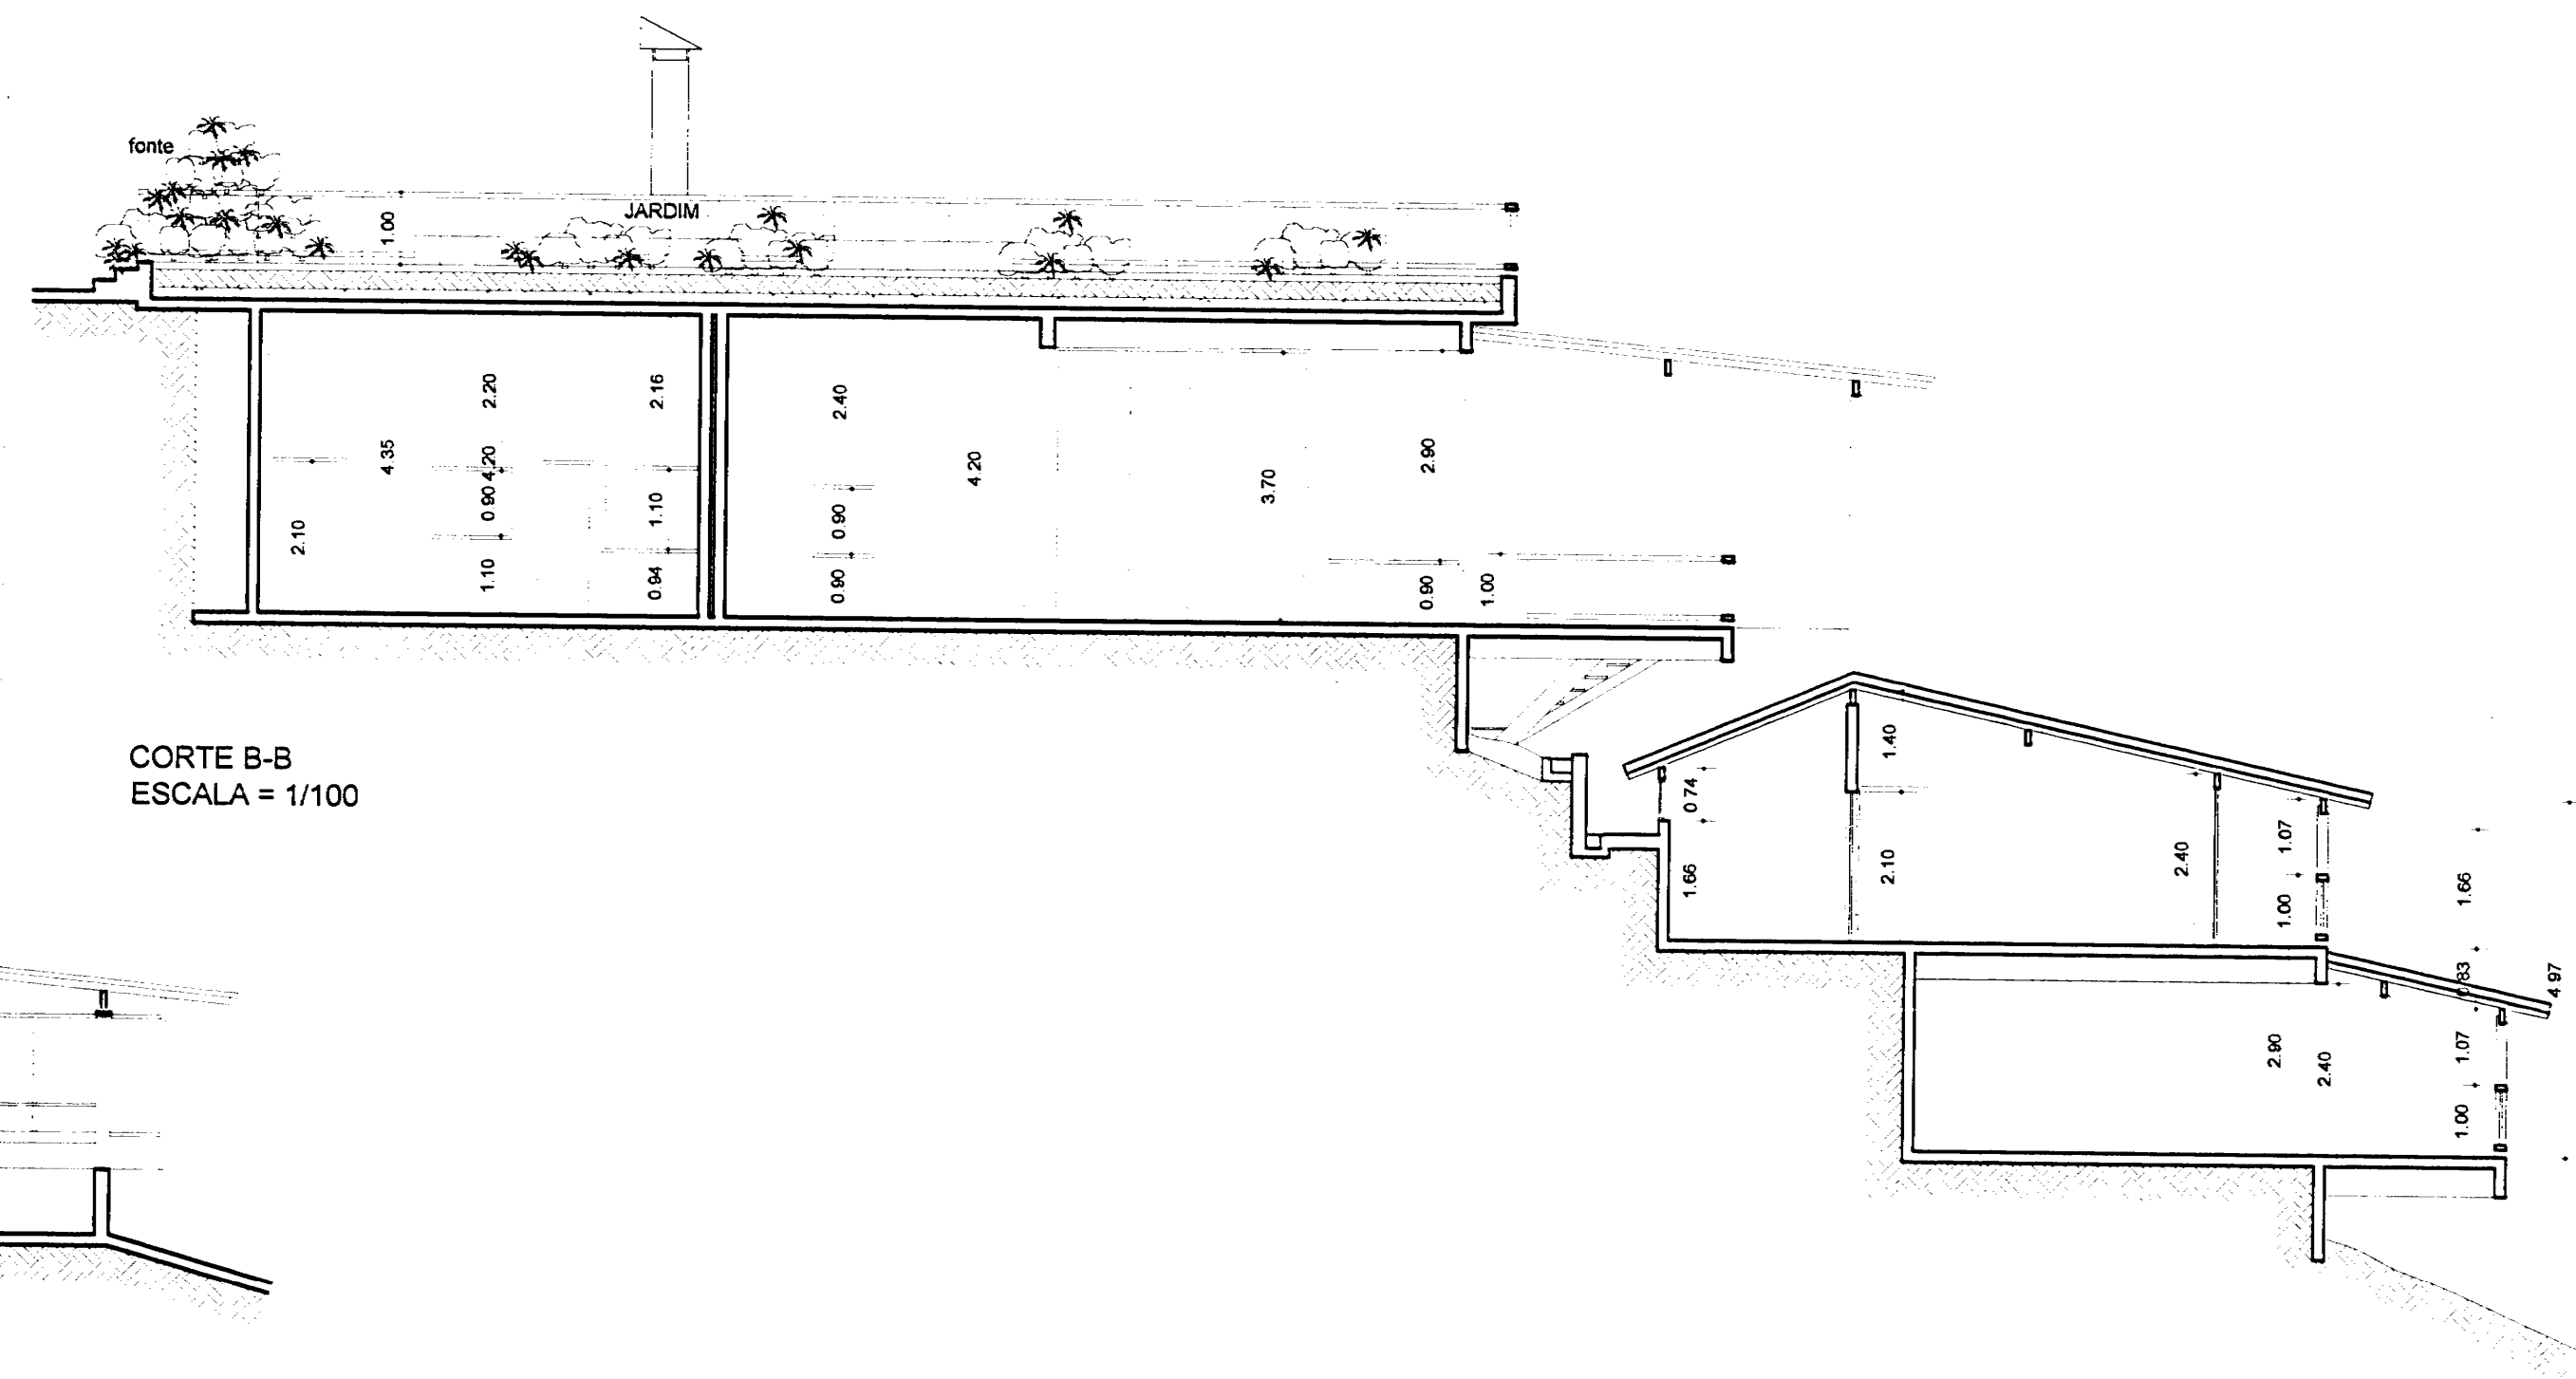

CORTE B-B
ESCALA = 1/100

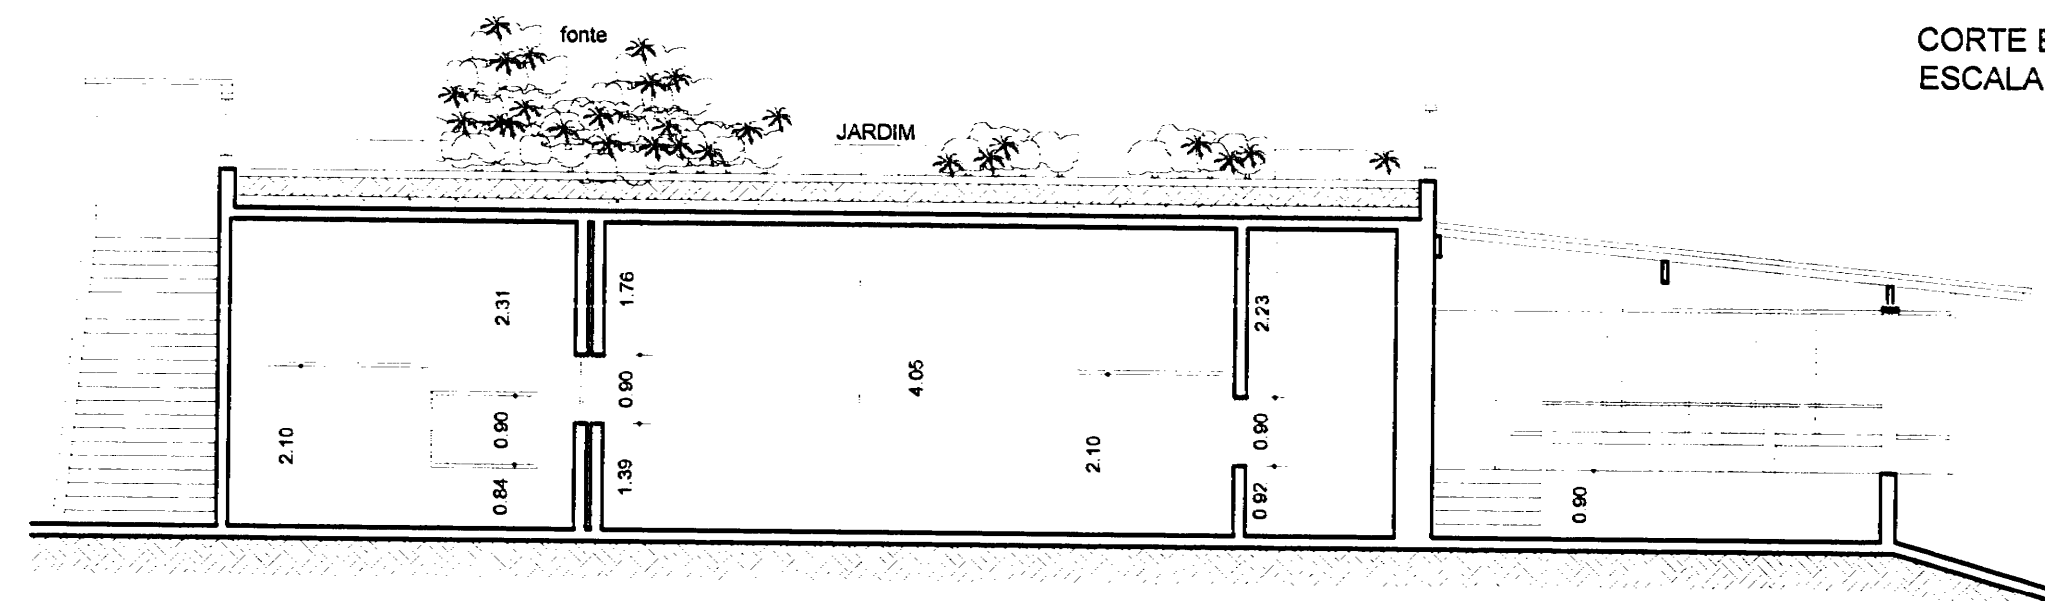

CORTE A-A
ESCALA = 1/100

Prefeitura Municipal de Nova Friburgo
Secretaria do Meio Ambiente
DEFERIDO
Processo nº 116.31/08
Nova Friburgo, 29 de agosto de 2008
Arquiteto: Roberto de Gouveia Vianna
Secretário do Meio Ambiente

PROJETO PARA LEGALIZAÇÃO DE ACRÉSCIMO DE
UMA CONSTRUÇÃO DESTINADA A UM SPA, SITO A
RUA VIRGINIA RIBEIRO, N° 1865, PARQUE WALTER
ZABEL, ALTO 50,

MURY - NOVA FRIBURGO - RJ.

Proprietário: Shami Gur, Suzanne Penn
Ametista Participações Ltda.
Projeto: Rogério Nogueira Kato - CREA 33.85 D RJ
Resp. técnico: Arquiteto

CORTES E FACHADA
ESTÚDIO / ESTAR / SUÍTES

data: MARÇO - 2008
escala: indicada
desenho em CAD: Max Araujo

Obs.: Este prancha só contém acréscimo