



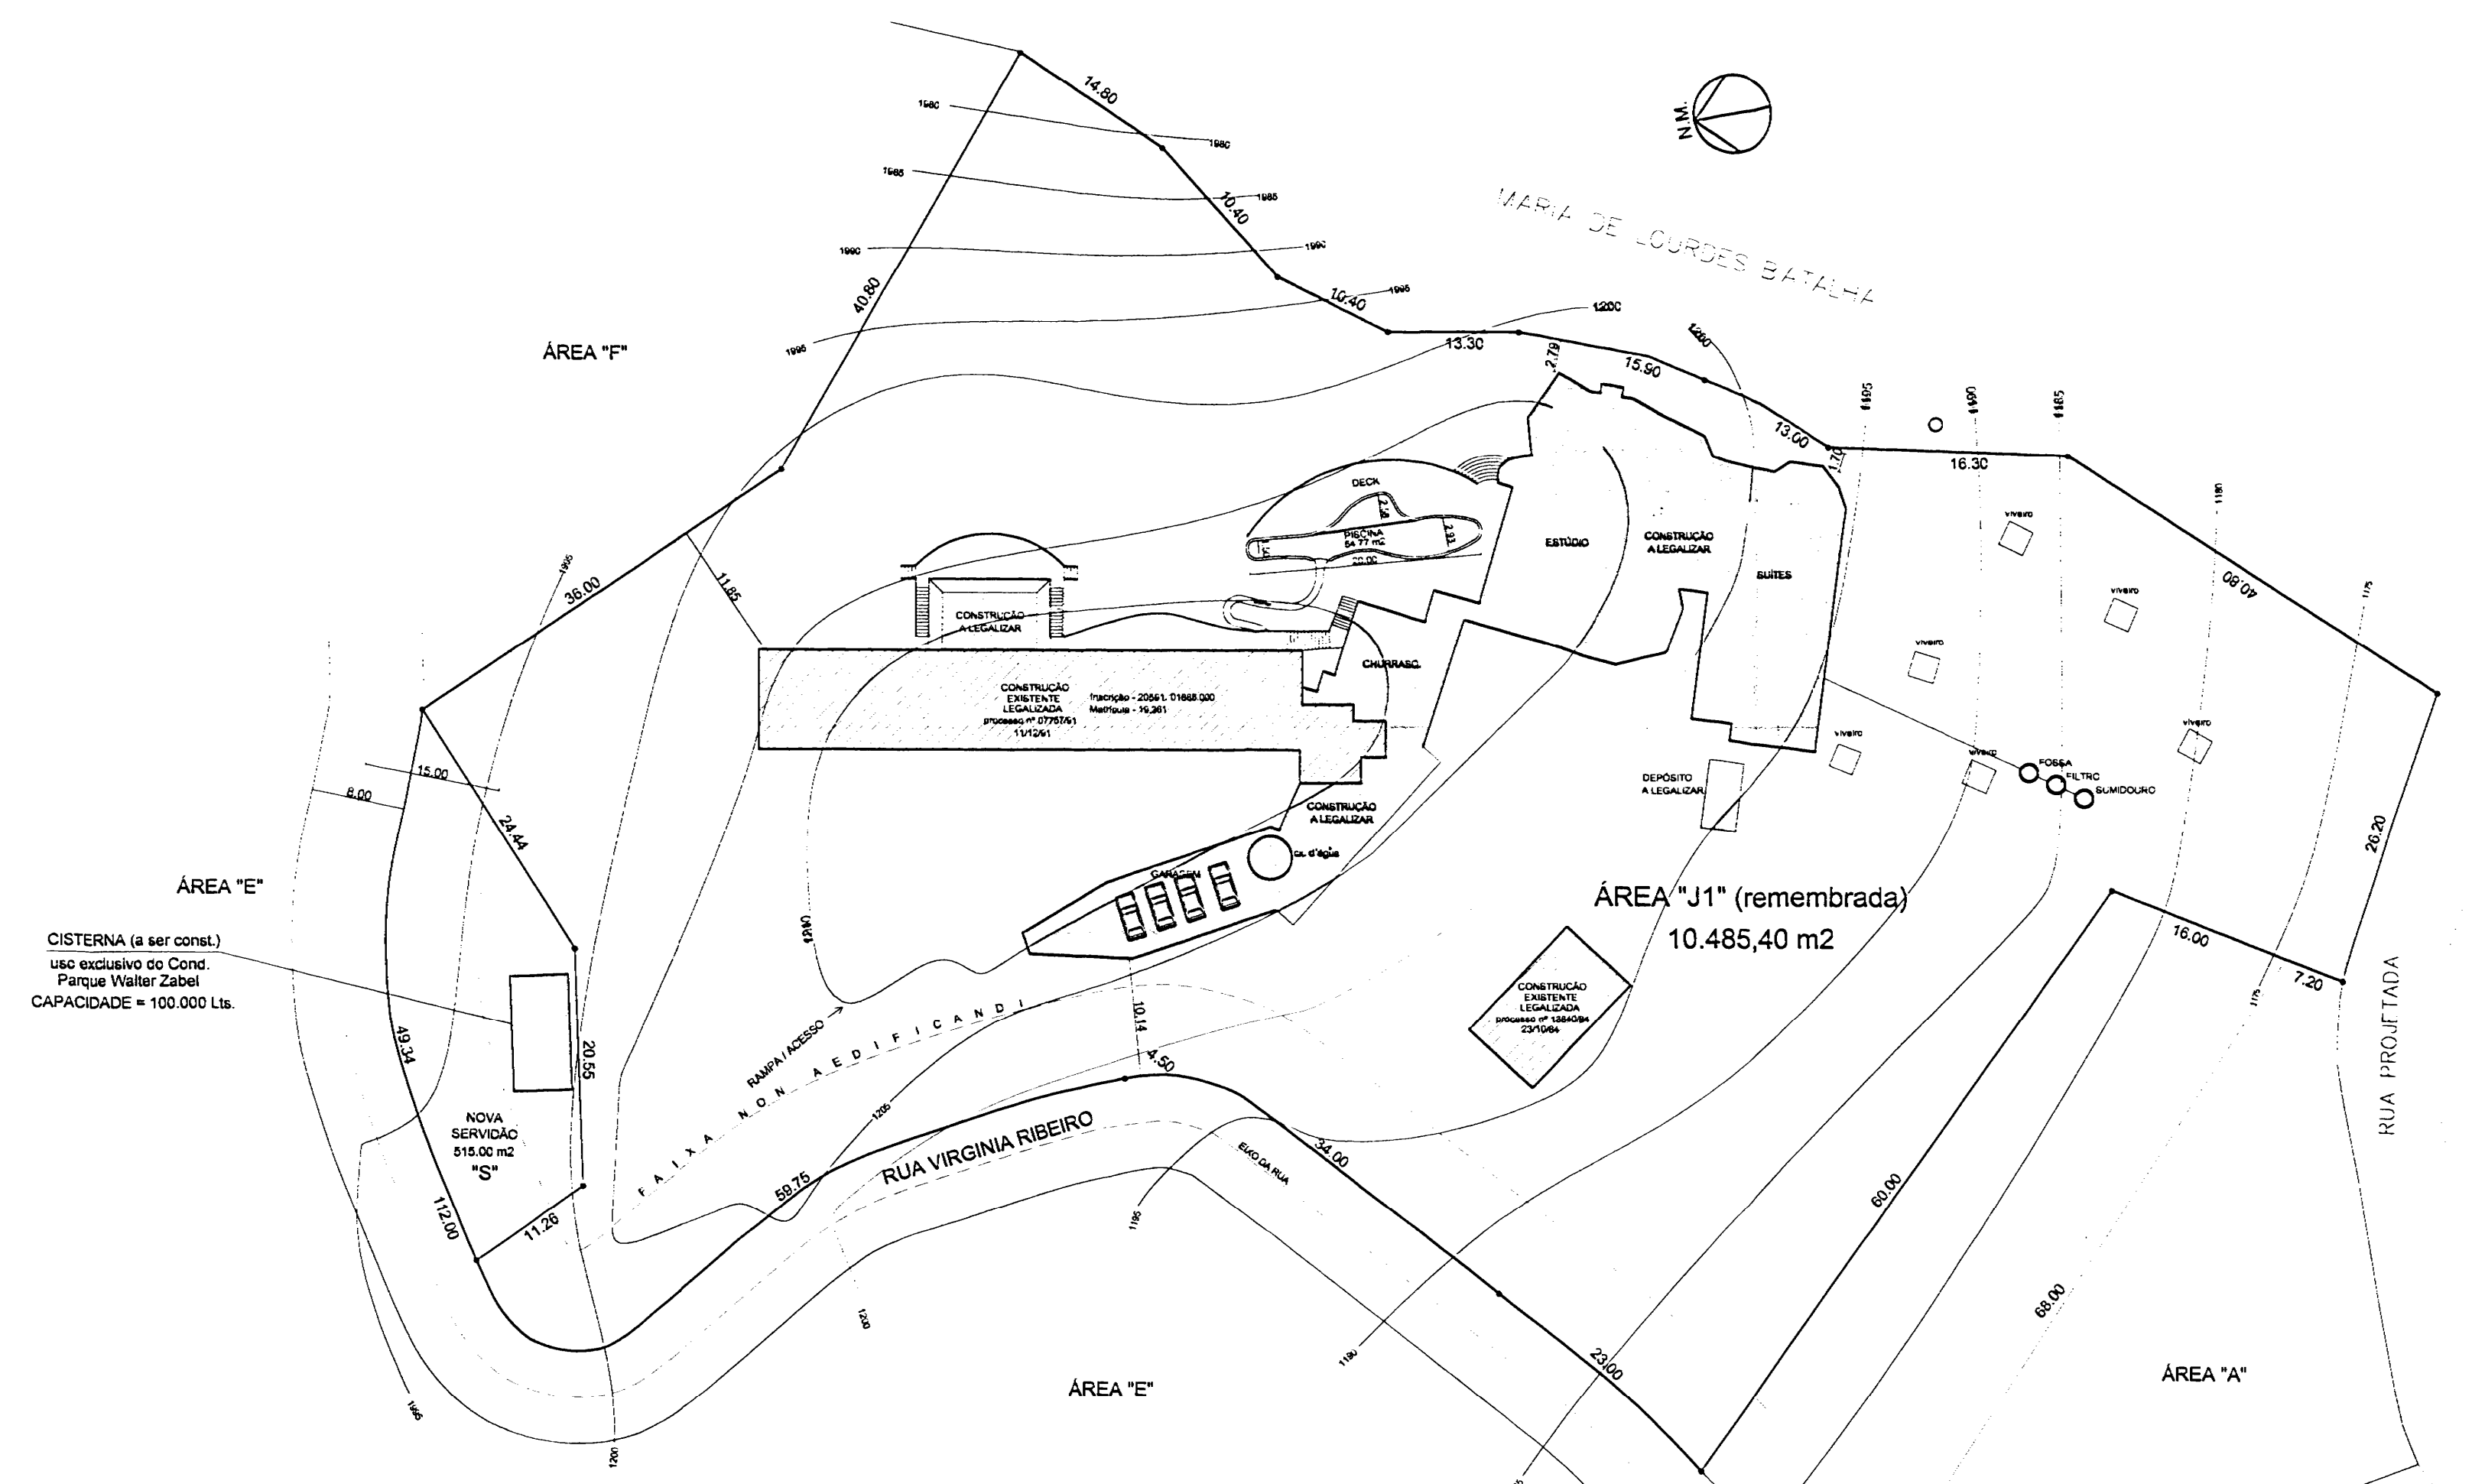

SITUAÇÃO
ESCALA = 1/500

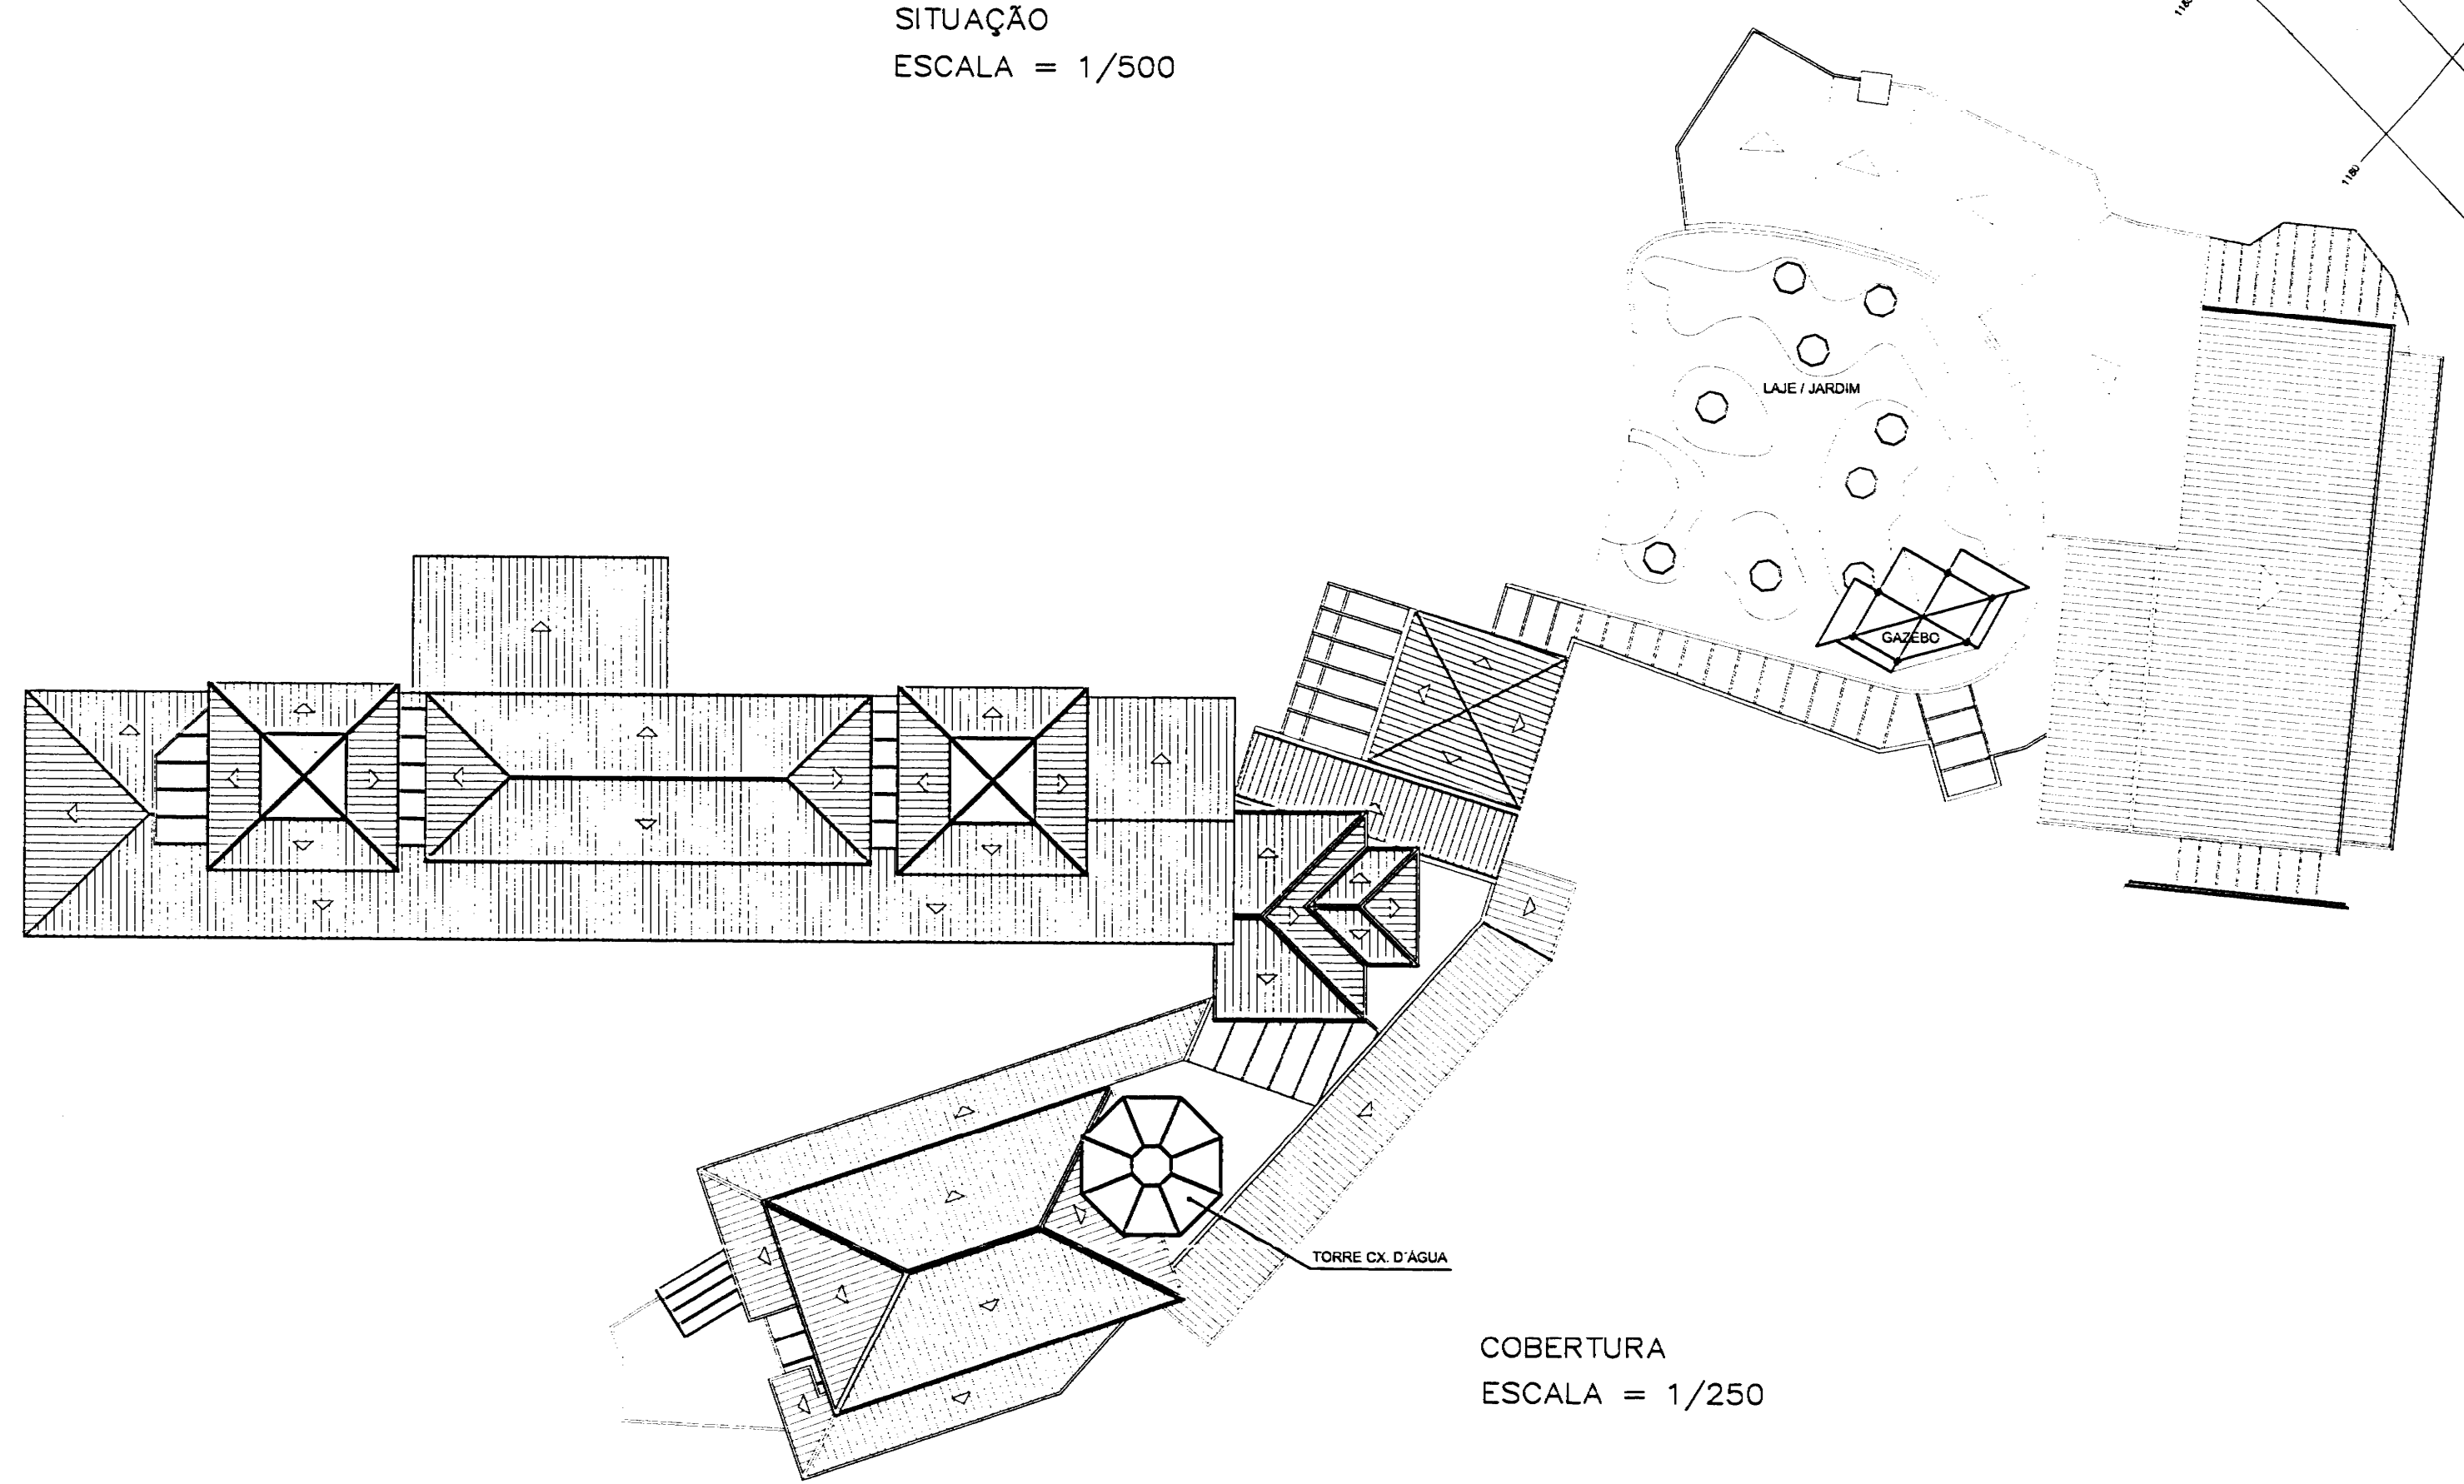

COBERTURA
ESCALA = 1/250

QUADRO DE ÁREAS	
ÁREA DE CONSTRUÇÃO EXISTENTE APROVADA	= 648,78 m2
ÁREA DE ACRÉSCIMO A LEGALIZAR	= 1.493,06 m2
ÁREA DE PROJEÇÃO	= 1.524,35 m2
TAXA DE OCUPAÇÃO	= 14,53 %
ÁREA TOTAL DO TERRENO	= 10.485,40 m2

Prefeitura Municipal de Nova Friburgo
Secretaria do Meio Ambiente
DEFERIDO
Processo nº 4631/08
Nova Friburgo: 29 de agosto de 2008
Arquit. Roberto de Gouveia Vianna
Secretaria do Meio Ambiente

PROJETO PARA LEGALIZAÇÃO DE ACRÉSCIMO DE
UMA CONSTRUÇÃO DESTINADA A UM SPA, SITO A
RUA VIRGINIA RIBEIRO, Nº 1865, PARQUE WALTER
ZABEL, ALTO 50,

MURY - NOVA FRIBURGO - RJ.

Proprietário: Shami Gur
Arquiteta Participações Ltda.
Suzanne Penny

Projeto: Rogério Viqueira Kato - CREA 33185 D RJ
Resp. técnico: Arquiteto

SITUAÇÃO E COBERTURA

data MARÇO - 2008	escala indicada	desenho em CAD Max Araujo
----------------------	--------------------	------------------------------

Obs.: